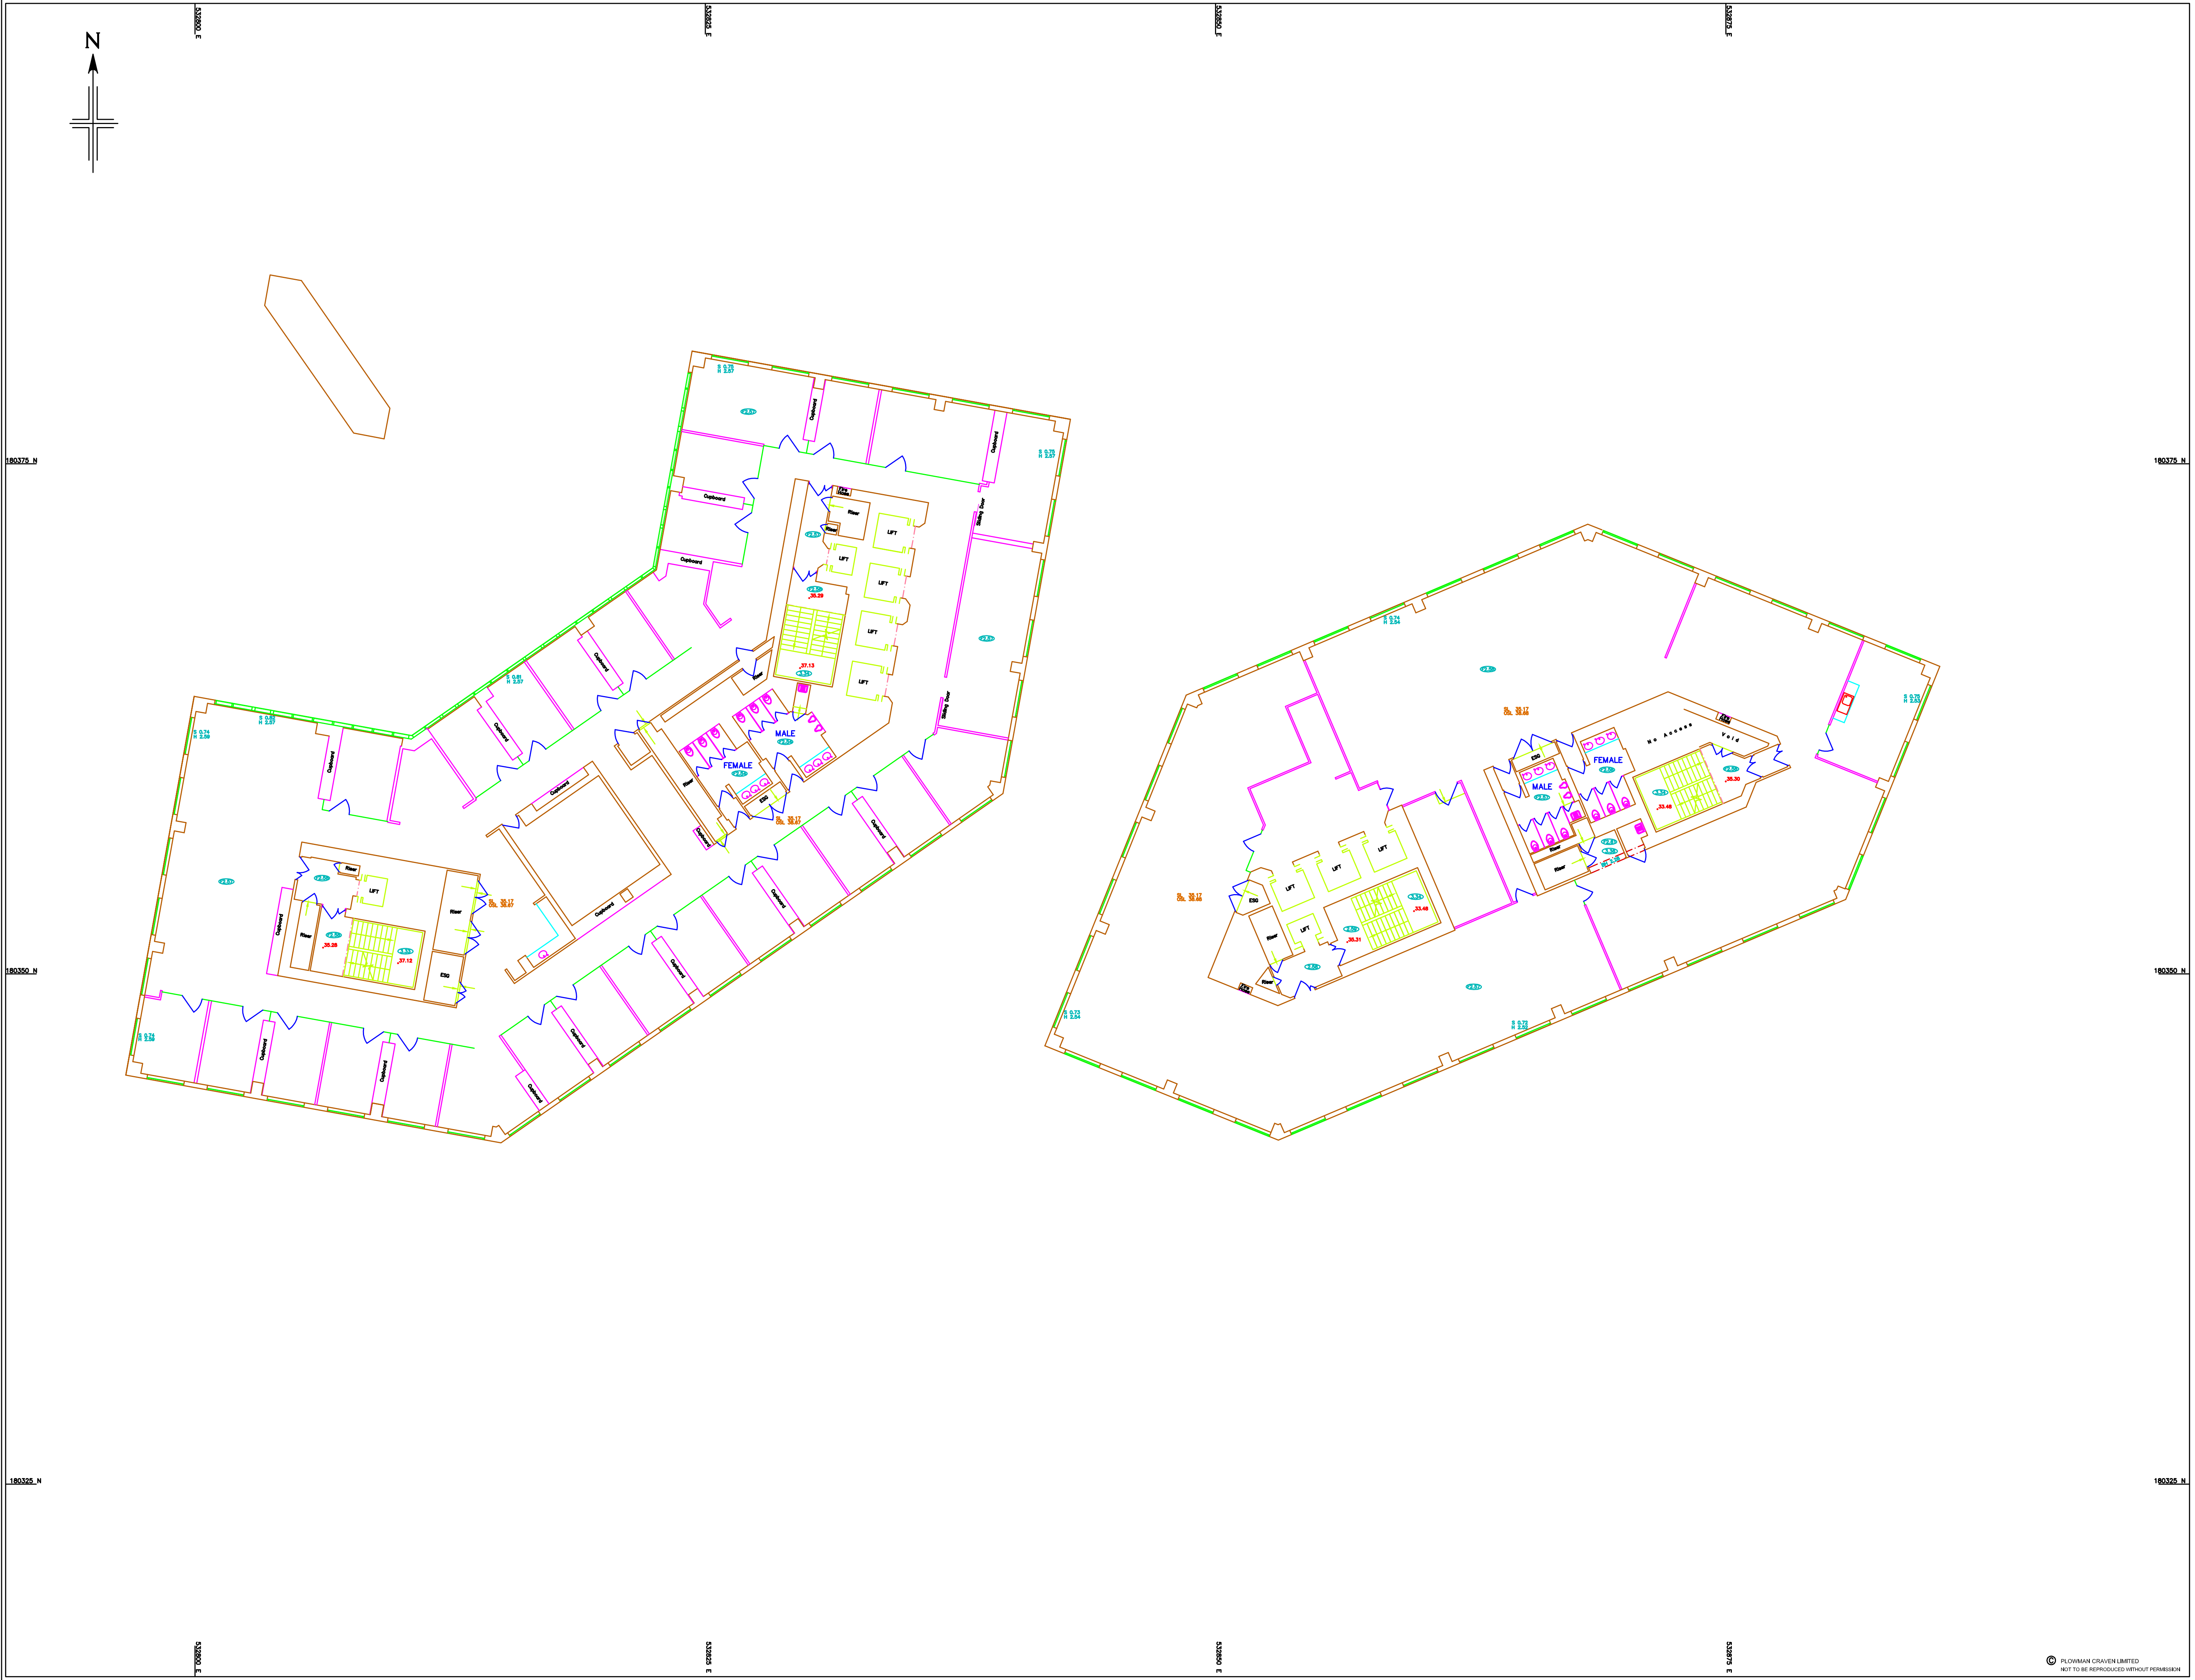

## STANDARD ABBREVIATIONS

| | | | |
|---|---|---|---|
| A/C | Air Conditioner | IRF | Iron Railing Fence |
| AH | Arch Height | IRS | Illuminated Road Sign |
| AL | Arch Level | JB | Junction Box |
| ASH | Arch Spring Height | L | Light |
| ASL | Arch Spring Level | LB | Litter Bin |
| B | Bollard | LP | Lamp Post |
| BGP | Break Glass Point | Max | Maximum |
| BH | Beam Height | MH | Manhole |
| Br | Brick | Min | Minimum |
| BRW | Brick Retaining Wall | O/H | Overhead |
| BSL | Beam Soffit Level | OSBM | Ordnance Survey Bench Mark |
| BT | British Telecom | OSL | Overhead Slab Level |
| BW | Brick Wall | P | Post |
| CBF | Close Boarded Fence | PB | Pillar Box |
| CCTV | Closed Circuit Television | PLt | Pavement Light |
| Chy | Chimney | PS | Paving Stones |
| CL | Cover Level | Rad | Radiator |
| CLF | Chain Link Fence | RDM | Recessed Door Mat |
| Col | Column | RE | Rodding Eye |
| Conc | Concrete | RS | Road Sign |
| CPS | Concrete Paving Slabs | RSJ | Rolled Steel Joist |
| CTV | Cable Television IC | RWP | Rain Water Pipe |
| Cup | Cupboard | s | spread |
| DP | Down Pipe | S | Window Sill Level/Height |
| DrC | Drainage Channel | SBM | Site Bench Mark |
| EIC | Electrical Inspection Cover | SC | Stop Cock |
| EJB | Electrical Junction Box | SH | Spring Height |
| EM | Electricity Meter | SL | Slab Level |
| ER | Earthing Rod | Slt | Skylight |
| ESG | Electrical Switchgear | SO | Smoke Outlet |
| FA | Fire Alarm | SP | Sign Post |
| FB | Flower Bed | SS | Security Sensor |
| FE | Fire Extinguisher | SV | Stop Valve |
| FH | Fire Hydrant | T | Telephone |
| FHR | Fire Hose Reel | Tac | Tactile Paving |
| FL | Floor Level | TBM | Temporary Bench Mark |
| Flt | Floodlight | TCB | Telephone Call Box |
| g | girth | TIC | Telephone Inspection Cover |
| G | Gully | TJB | Telephone Junction Box |
| GC | Gas Cock | TL | Traffic Light |
| GM | Gas Meter | TLCB | Traffic Light Control Box |
| GV | Gas Valve | TLIC | Traffic Light Inspection Cover |
| H | Window Head Height/Level | TP | Telephone Pole |
| h | height | Typ | Typical |
| HB | Hand Basin | V | Vent |
| HR | Handrail | VP | Vent Pipe |
| IC | Inspection Cover | WH | Water Heater |
| IL | Invert Level | WM | Water Meter |
| | | WV | Water Valve |

## OTHER ABBREVIATIONS

## LEGEND

| | |
|---|---|
| 2.70 | FLOOR TO CEILING HEIGHT |
| F2.70 | FLOOR TO FALSE CEILING HEIGHT |
| 2.70 | CEILING LEVEL |
| SL 2.70 | SLAB LEVEL |
| OSL 2.70 | OVERHEAD SLAB LEVEL |
| — · — · — | OVERHEAD DETAIL |
| — — — | ASSUMED |
| → | ALL ARROWS POINT UP UNLESS OTHERWISE STATED OR ON ROOFS |
| ▷ | SLOPING CEILING ARROWS POINT UP |
| ¦→¦ | RAMP |

DUE TO THE INHERENT INSTABILITY OF PAPER MATERIALS, DRAWINGS PLOTTED ON PAPER MAY BE STRETCHED AND DISTORTED. DIMENSIONS SCALED FROM PAPER PLOTS SHOULD THEREFORE BE TREATED WITH CAUTION.

This drawing has been produced for the purpose of the original commissioning agent. Plowman Craven Limited will accept no responsibility for details that are subsequently found to be the consequence of undisclosed facts or that were obscured from view at the time of survey or that have been altered since the survey. All data remains the property of Plowman Craven Limited until full payment has been received.

See www.plowmancraven.co.uk for full terms and conditions of contract.

## ISSUES & REVISIONS

| Issue | Details | By | Date |
|---|---|---|---|
| A prov 1 | Drawing incomplete and unchecked | PCL | 25/03/11 |
| A | Final data | PCL | 28/04/11 |
| B | Slab and ceiling levels added | PCL | 01/06/11 |

## SHEET LAYOUT

THIS SURVEY HAS BEEN CARRIED OUT TO AN ACCURACY CONSISTENT WITH A PRESENTATION SCALE OF 1:100. INTERROGATED DIMENSIONS WILL BE WITHIN THE TOLERANCE ASSOCIATED WITH THIS AND SMALLER SCALES ONLY.

ALL LEVELS ARE IN METRES AND ARE ABOVE ORDNANCE SURVEY NEWLYN DATUM DERIVED BY MULTIPLE NETWORK RTK GPS OBSERVATIONS.

THE SURVEY GRID SHOWN ON THIS DRAWING IS POSITIONED ON ORDNANCE SURVEY (OS) NATIONAL GRID, OBTAINED BY MULTIPLE NETWORK RTK GPS OBSERVATIONS.

ALL QUOTED DIMENSIONS ARE IN METRES

DRAWING UNITS ARE METRES

CLIENT

ST MARTINS PROPERTY INVESTMENTS LIMITED
SHACKLETON HOUSE
4 BATTLEBRIDGE LANE
LONDON BRIDGE CITY
LONDON
SE1 2HX

JOB TITLE

# No 1 LONDON BRIDGE

LONDON BRIDGE CITY

## EIGHTH FLOOR PLAN

SURVEYED AND DRAWN BY

**Plowman Craven**
141 Lower Luton Road
Harpenden
Hertfordshire
AL5 5EQ

● +44(0)1582 765566
● +44(0)1582 765370
● info@plowmancraven.co.uk
● www.plowmancraven.co.uk

PRESENTATION SCALE 1:100 @ A0

DATE OF ORIGINAL SURVEY 25th March 2011

PC JOB No. 24571

CHECKED DGR

DRAWING No. 24730F-LB-10

ISSUE B

© PLOWMAN CRAVEN LIMITED
NOT TO BE REPRODUCED WITHOUT PERMISSION