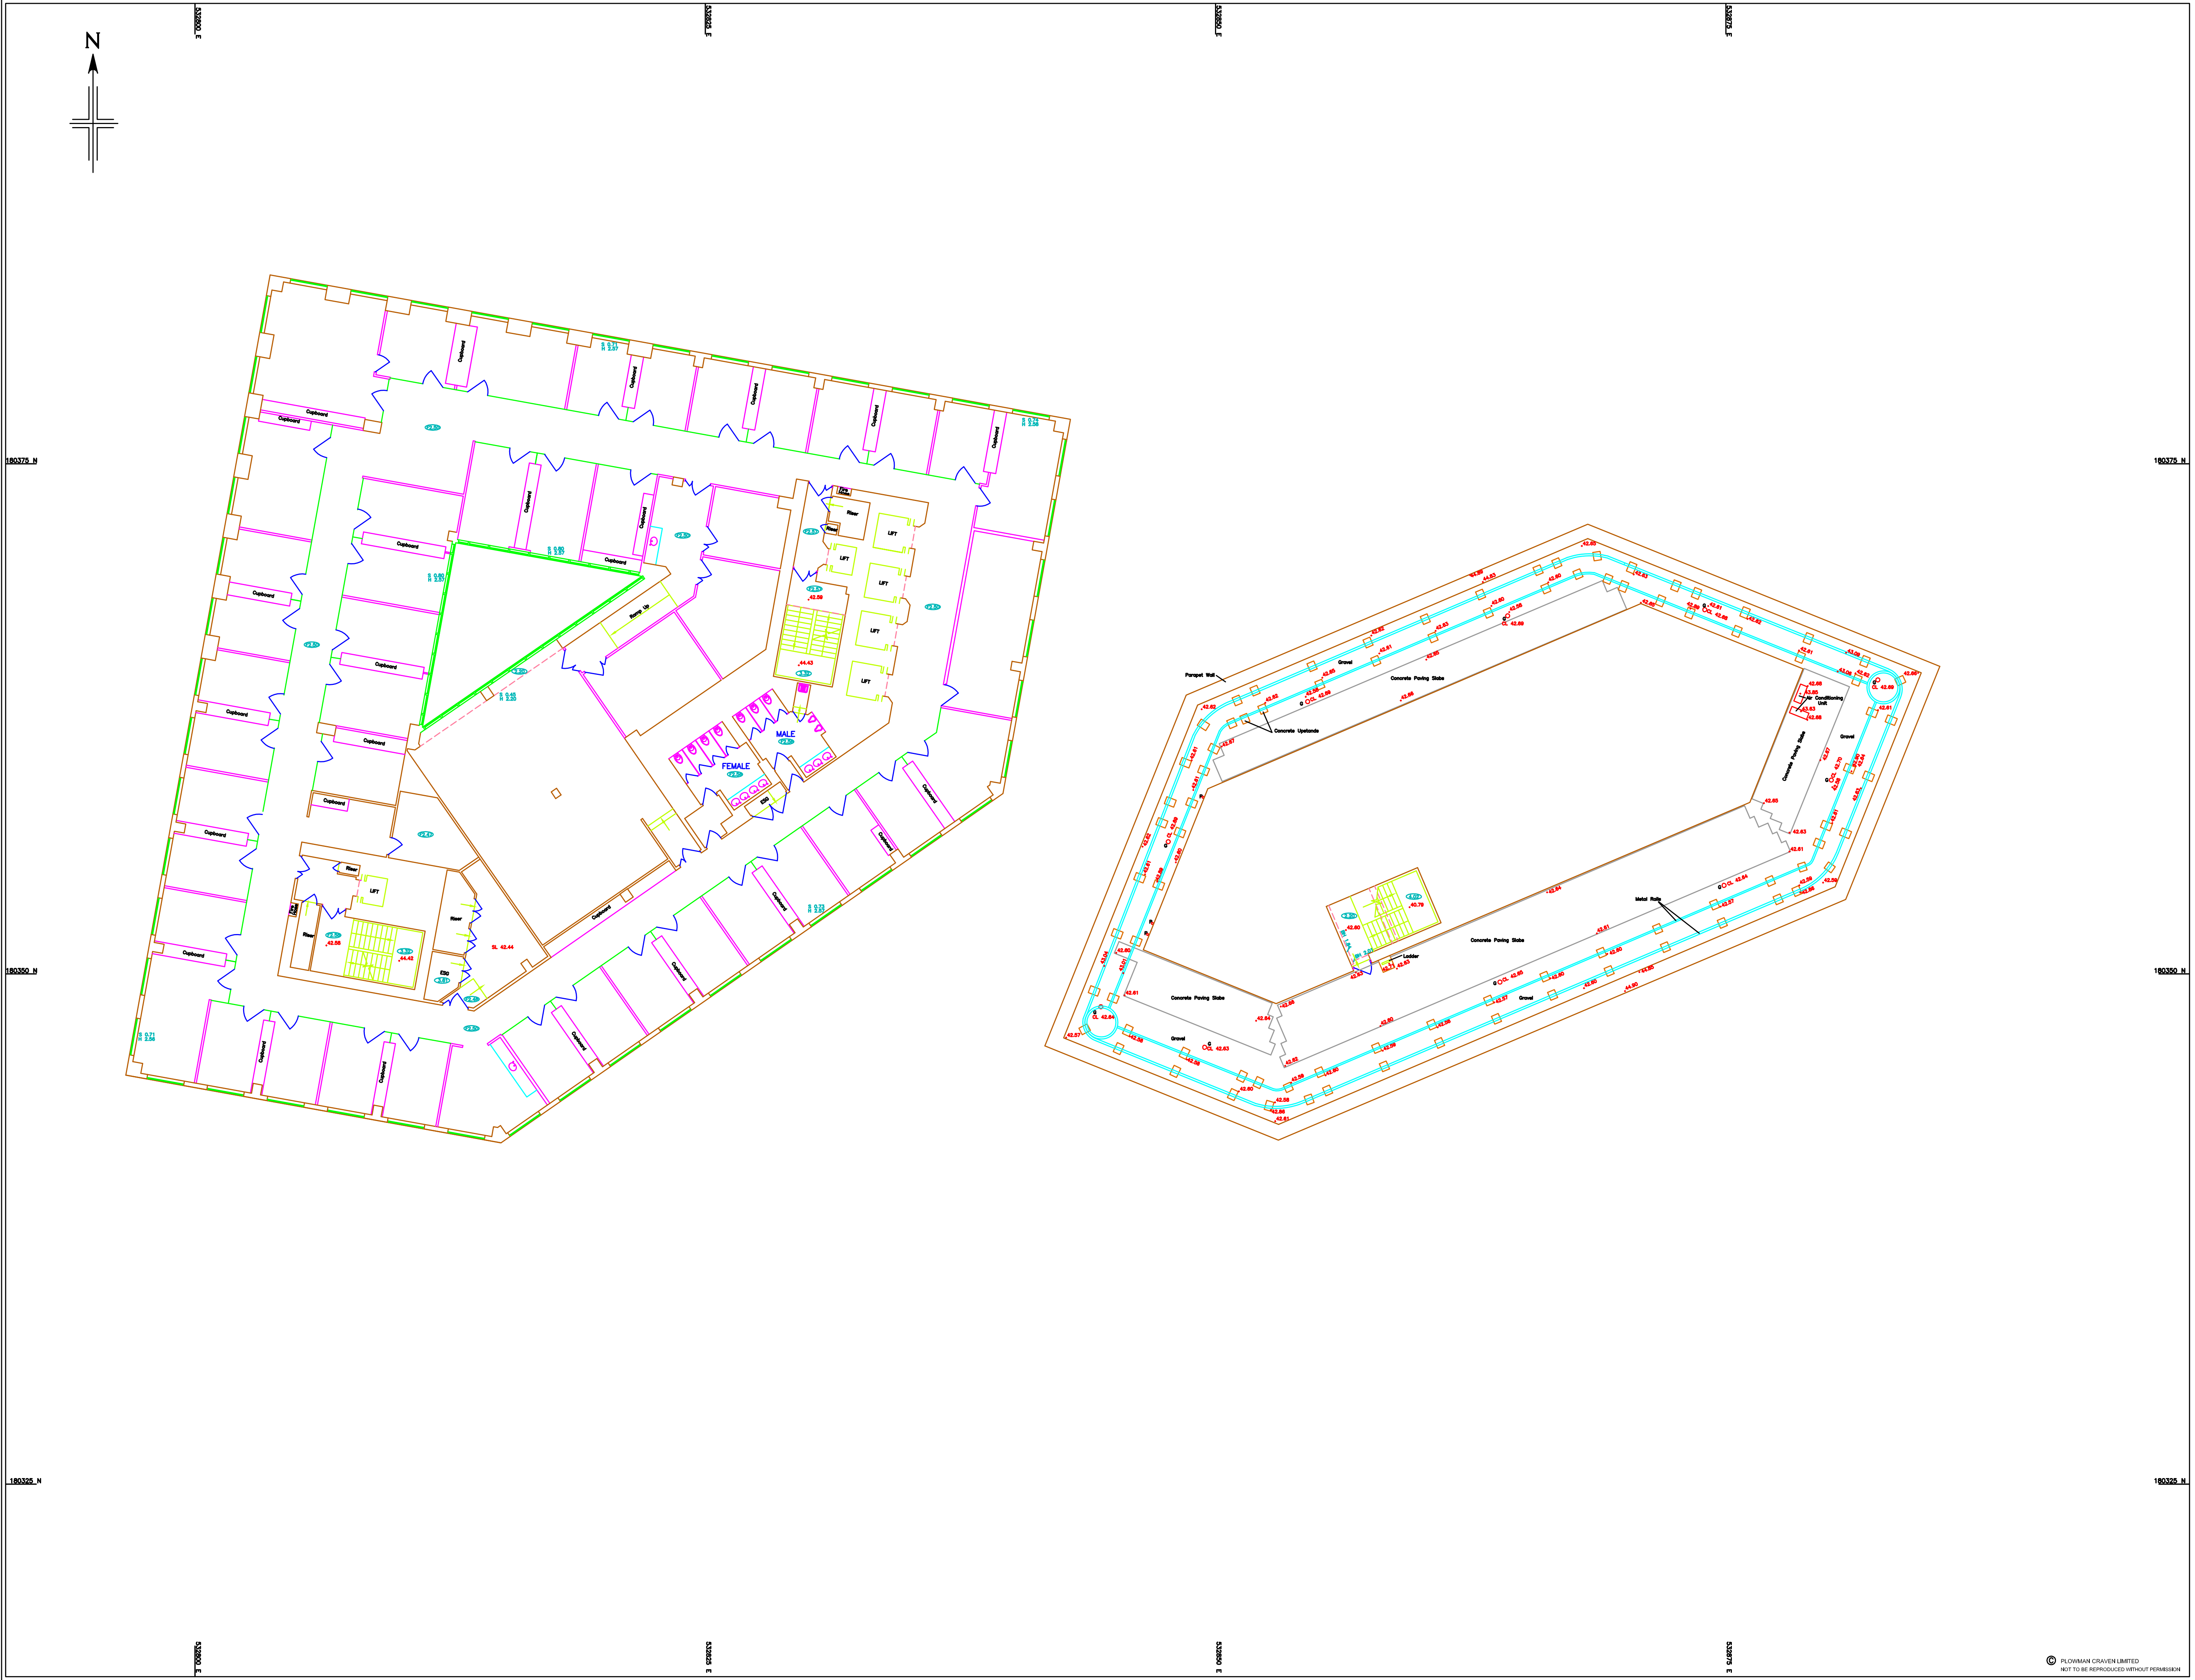

STANDARD ABBREVIATIONS

A/C	Air Conditioner	IRF	Iron Railing Fence
AH	Arch Height	IRS	Illuminated Road Sign
AL	Arch Level	JB	Junction Box
ASH	Arch Spring Height	L	Light
ASL	Arch Spring Level	LB	Litter Bin
B	Bollard	LP	Lamp Post
BGP	Break Glass Point	Max	Maximum
BH	Beam Height	MH	Manhole
Br	Brick	Min	Minimum
BRW	Brick Retaining Wall	O/H	Overhead
BSL	Beam Soffit Level	OSBM	Ordnance Survey Bench Mark
BT	British Telecom	OSL	Overhead Slab Level
BW	Brick Wall	P	Post
CBF	Close Boarded Fence	PB	Pillar Box
CCTV	Closed Circuit Television	PLt	Pavement Light
Chy	Chimney	PS	Paving Stones
CL	Cover Level	Rad	Radiator
CLF	Chain Link Fence	RDM	Recessed Door Mat
Col	Column	RE	Rodding Eye
Conc	Concrete	RS	Road Sign
CPS	Concrete Paving Slabs	RSJ	Rolled Steel Joist
CTV	Cable Television IC	RWP	Rain Water Pipe
Cup	Cupboard	s	spread
DP	Down Pipe	S	Window Sill Level/Height
DrC	Drainage Channel	SBM	Site Bench Mark
EIC	Electrical Inspection Cover	SC	Stop Cock
EJB	Electrical Junction Box	SH	Spring Height
EM	Electricity Meter	SL	Slab Level
ER	Earthing Rod	Slt	Skylight
ESG	Electrical Switchgear	SO	Smoke Outlet
FA	Fire Alarm	SP	Sign Post
FB	Flower Bed	SS	Security Sensor
FE	Fire Extinguisher	SV	Stop Valve
FH	Fire Hydrant	T	Telephone
FHR	Fire Hose Reel	Tac	Tactile Paving
FL	Floor Level	TBM	Temporary Bench Mark
Flt	Floodlight	TCB	Telephone Call Box
g	girth	TIC	Telephone Inspection Cover
G	Gully	TJB	Telephone Junction Box
GC	Gas Cock	TL	Traffic Light
GM	Gas Meter	TLCB	Traffic Light Control Box
GV	Gas Valve	TLIC	Traffic Light Inspection Cover
H	Window Head Height/Level	TP	Telephone Pole
h	height	Typ	Typical
HB	Hand Basin	V	Vent
HR	Handrail	VP	Vent Pipe
IC	Inspection Cover	WH	Water Heater
IL	Invert Level	WM	Water Meter
		WV	Water Valve

OTHER ABBREVIATIONS

LEGEND

(2.70)	FLOOR TO CEILING HEIGHT
(F2.70)	FLOOR TO FALSE CEILING HEIGHT
[2.70]	CEILING LEVEL
SL 2.70	SLAB LEVEL
OSL 2.70	OVERHEAD SLAB LEVEL
— · — · —	OVERHEAD DETAIL
— — —	ASSUMED
——►	ALL ARROWS POINT UP UNLESS OTHERWISE STATED OR ON ROOFS
——▷	SLOPING CEILING ARROWS POINT UP
|——►|	RAMP

DUE TO THE INHERENT INSTABILITY OF PAPER MATERIALS, DRAWINGS PLOTTED ON PAPER MAY BE STRETCHED AND DISTORTED. DIMENSIONS SCALED FROM PAPER PLOTS SHOULD THEREFORE BE TREATED WITH CAUTION.

This drawing has been produced for the purpose of the original commissioning agent. Plowman Craven Limited will accept no responsibility for details that are subsequently found to be the consequence of undisclosed facts or that were obscured from view at the time of survey or that have been altered since the survey. All data remains the property of Plowman Craven Limited until full payment has been received.

See www.plowmancraven.co.uk for full terms and conditions of contract.

ISSUES & REVISIONS

Issue	Details	By	Date
A prov 1	Drawing incomplete and unchecked	PCL	25/03/11
A	Final data	PCL	28/04/11
B	Slab and ceiling levels added	PCL	01/06/11
C	Roof detail added	PCL	20/07/11

SHEET LAYOUT

THIS SURVEY HAS BEEN CARRIED OUT TO AN ACCURACY CONSISTENT WITH A PRESENTATION SCALE OF 1:100. INTERROGATED DIMENSIONS WILL BE WITHIN THE TOLERANCE ASSOCIATED WITH THIS AND SMALLER SCALES ONLY.

ALL LEVELS ARE IN METRES AND ARE ABOVE ORDNANCE SURVEY NEWLYN DATUM DERIVED BY MULTIPLE NETWORK RTK GPS OBSERVATIONS.

THE SURVEY GRID SHOWN ON THIS DRAWING IS POSITIONED ON ORDNANCE SURVEY (OS) NATIONAL GRID, OBTAINED BY MULTIPLE NETWORK RTK GPS OBSERVATIONS.

ALL QUOTED DIMENSIONS ARE IN METRES

DRAWING UNITS ARE METRES

CLIENT

ST MARTINS PROPERTY INVESTMENTS LIMITED

SHACKLETON HOUSE
4 BATTLEBRIDGE LANE
LONDON BRIDGE CITY
LONDON
SE1 2HX

JOB TITLE

No 1 LONDON BRIDGE

LONDON BRIDGE CITY

TENTH FLOOR PLAN

SURVEYED AND DRAWN BY

Plowman Craven

141 Lower Luton Road
Harpenden
Hertfordshire
AL5 5EQ

● +44(0)1582 765566 ● info@plowmancraven.co.uk
● +44(0)1582 765370 ● www.plowmancraven.co.uk

PRESENTATION SCALE	1:100 @ A0		
DATE OF ORIGINAL SURVEY	25th March 2011		
PC JOB No.	24571	CHECKED	DGR
DRAWING No.	24571F-LB-12		
ISSUE	C		

© PLOWMAN CRAVEN LIMITED
NOT TO BE REPRODUCED WITHOUT PERMISSION