

Knight Controls Limited
8 The Maltings Industrial Estate
Maltings Road
Battlesbridge
Essex
SS11 7RH
Tel: 01245 808218
www.knightcontrols.co.uk


Smart Managed Solutions
Unit 1 Boyd Business Centre
Whitewall Road
Rochester
Kent
ME2 4DZ
Tel: 020 3196 4903
www.smartmanagedsolutions.co.uk

2 More London
Floor Layout Drawings

REVISION	DESCRIPTION	DATE	DRAWN
0	Original Issue	Nov 25	B Janosz

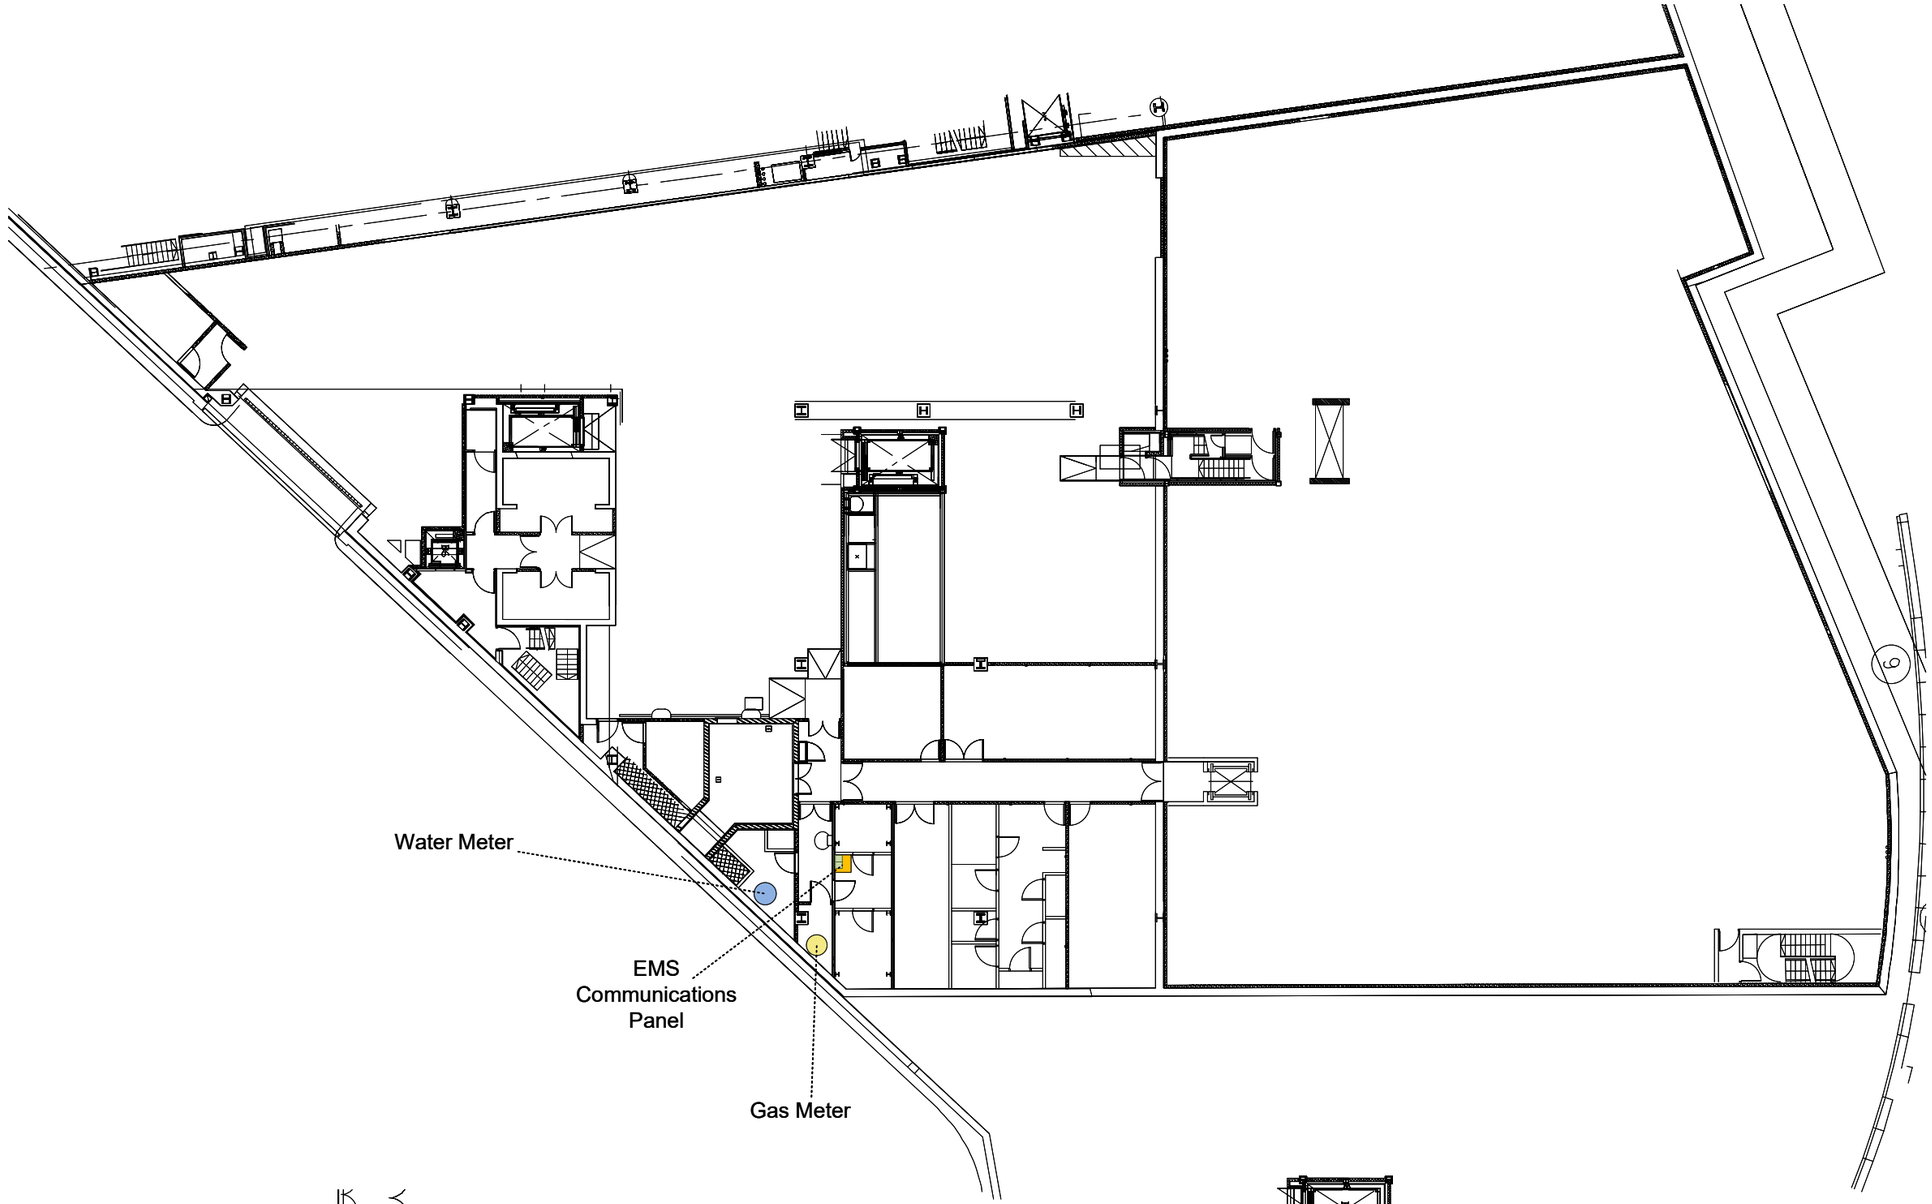

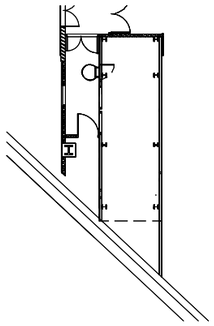

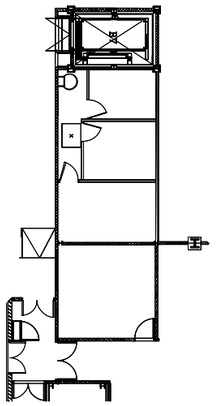

Legend

- CAT 5/6 Cables
- Modbus Network
- Electricity Meters
- Heat Meters
- Water Meters
- Gas Meters
- Modbus Gateway
- Distribution Board


knight CONTROLS ENERGY


Knight Controls Limited
8 Maltings Industrial Estate
Maltings Road
Battlesbridge
Essex
SS11 7RH
www.knightcontrols.co.uk

TITLE::

Lower Ground Floor

SITE: 2 More London	DRAWING No: 161225	REVISION: 0
CLIENT: Smart Managed Solutions	DATE: December 2025	SHEET: 2 of 13

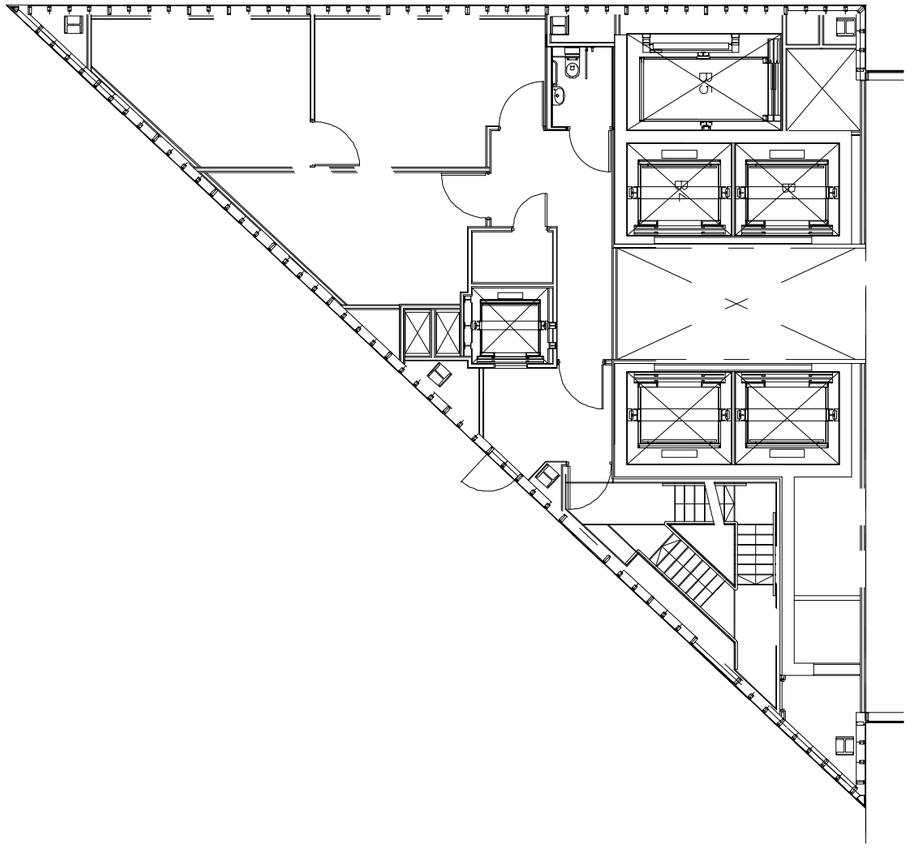

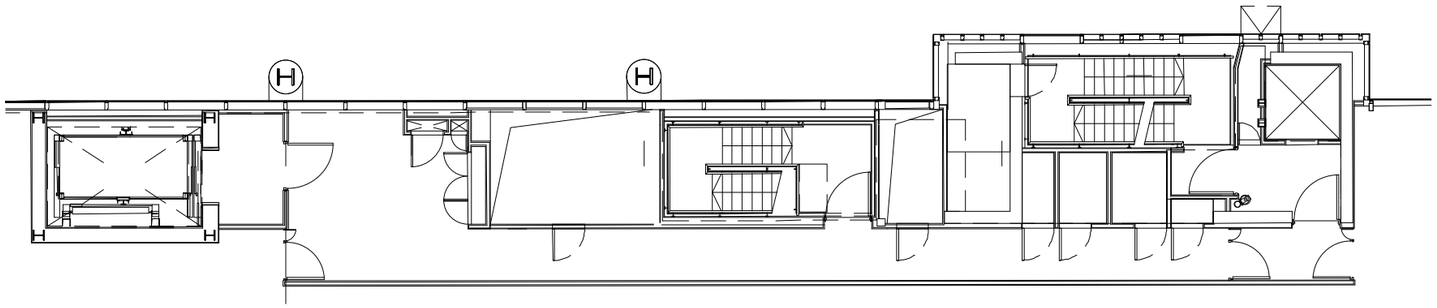

Legend

- CAT 5/6 Cables
- Modbus Network
- Electricity Meters
- Heat Meters
- Water Meters
- Gas Meters
- Modbus Gateway
- Distribution Board


knight CONTROLS ENERGY

Knight Controls Limited
8 Maltings Industrial Estate
Maltings Road
Battlesbridge
Essex
SS11 7RH
www.knightcontrols.co.uk

TITLE::

Mezzanine Floor

SITE: **2 More London**	DRAWING No: 161225	REVISION: 0
CLIENT: **Smart Managed Solutions**	DATE: December 2025	SHEET: 3 of 13

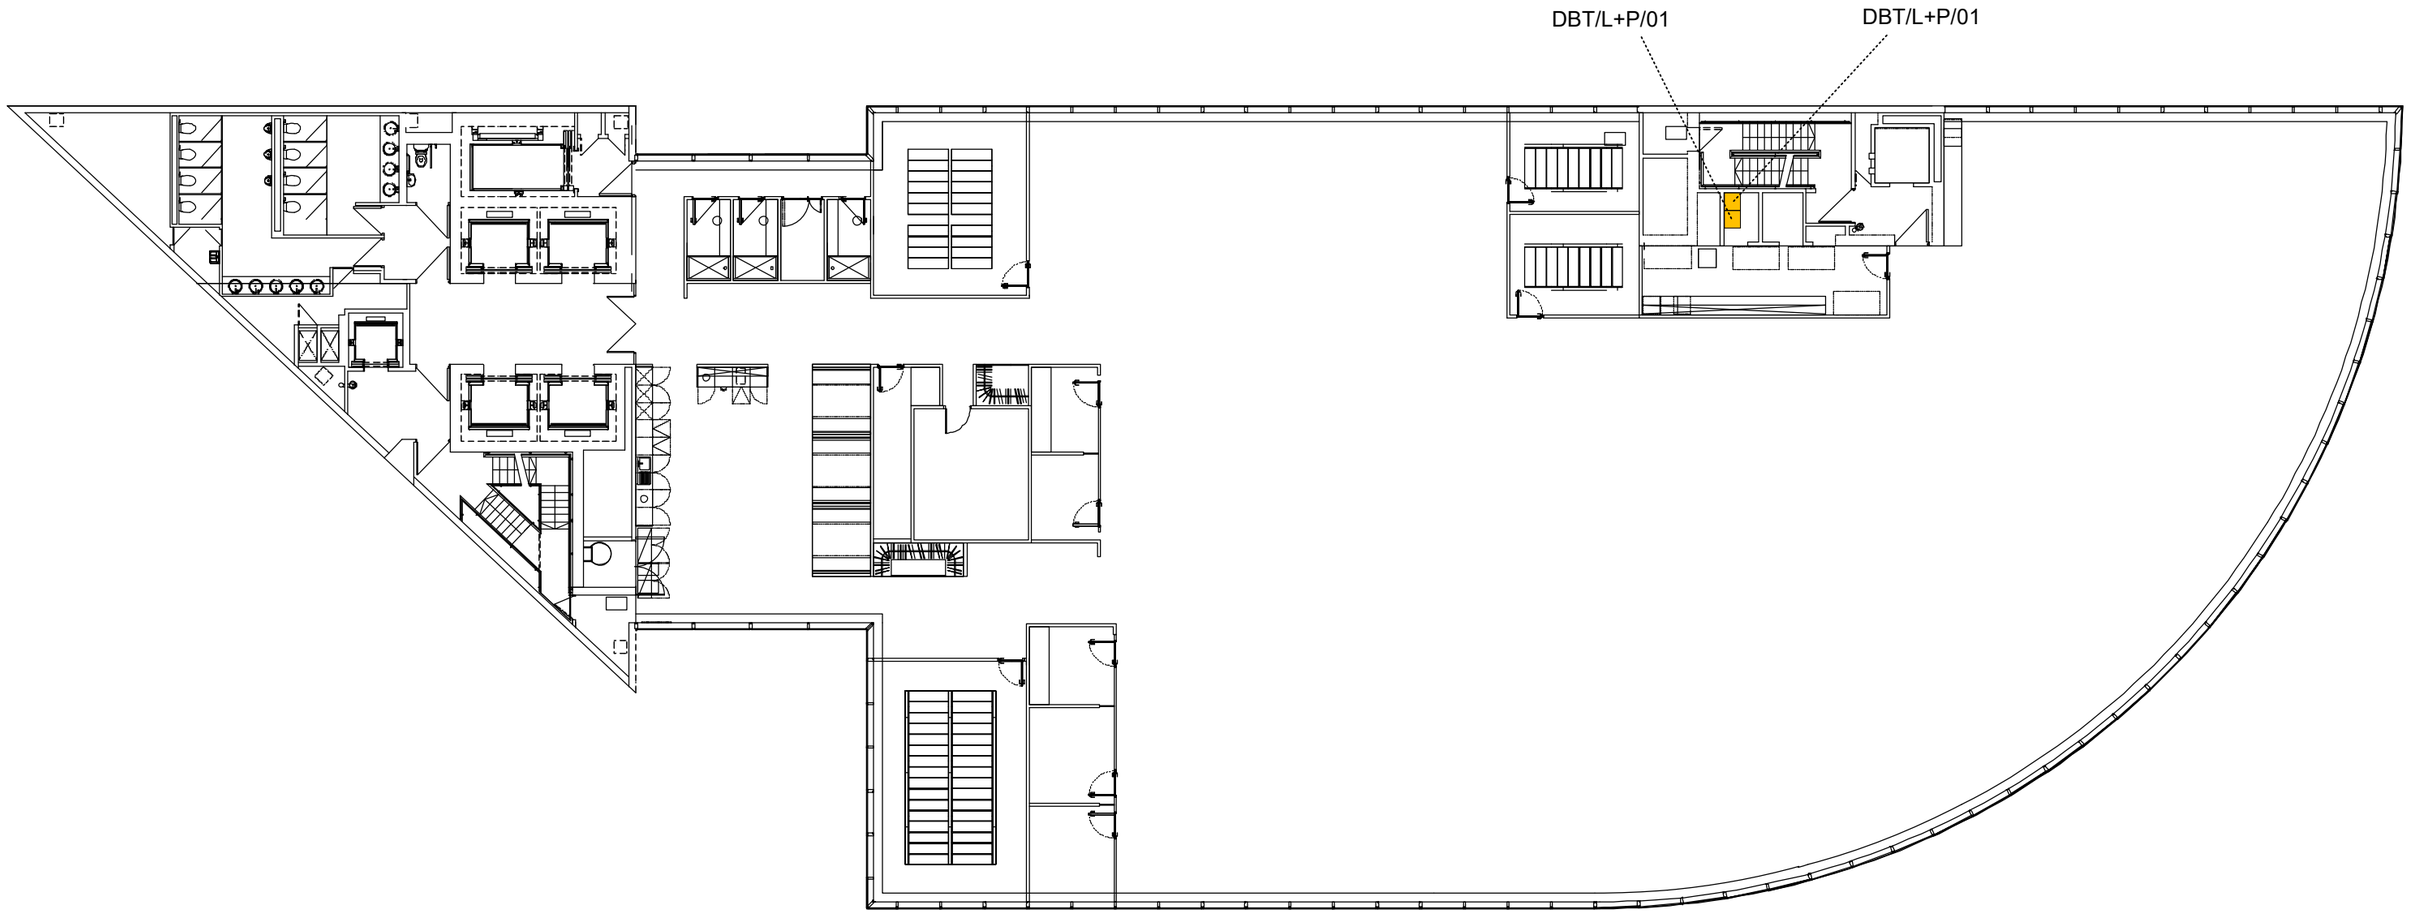

Legend


- CAT 5/6 Cables
- Modbus Network
- Electricity Meters
- Heat Meters
- Water Meters
- Gas Meters
- Modbus Gateway
- Distribution Board

Knight Controls Limited
8 Maltings Industrial Estate
Maltings Road
Battlesbridge
Essex
SS11 7RH
www.knightcontrols.co.uk

TITLE::

Level 1

SITE:	DRAWING No:	REVISION:
2 More London	161225	0
CLIENT:	DATE:	SHEET:
Smart Managed Solutions	December 2025	4 of 13

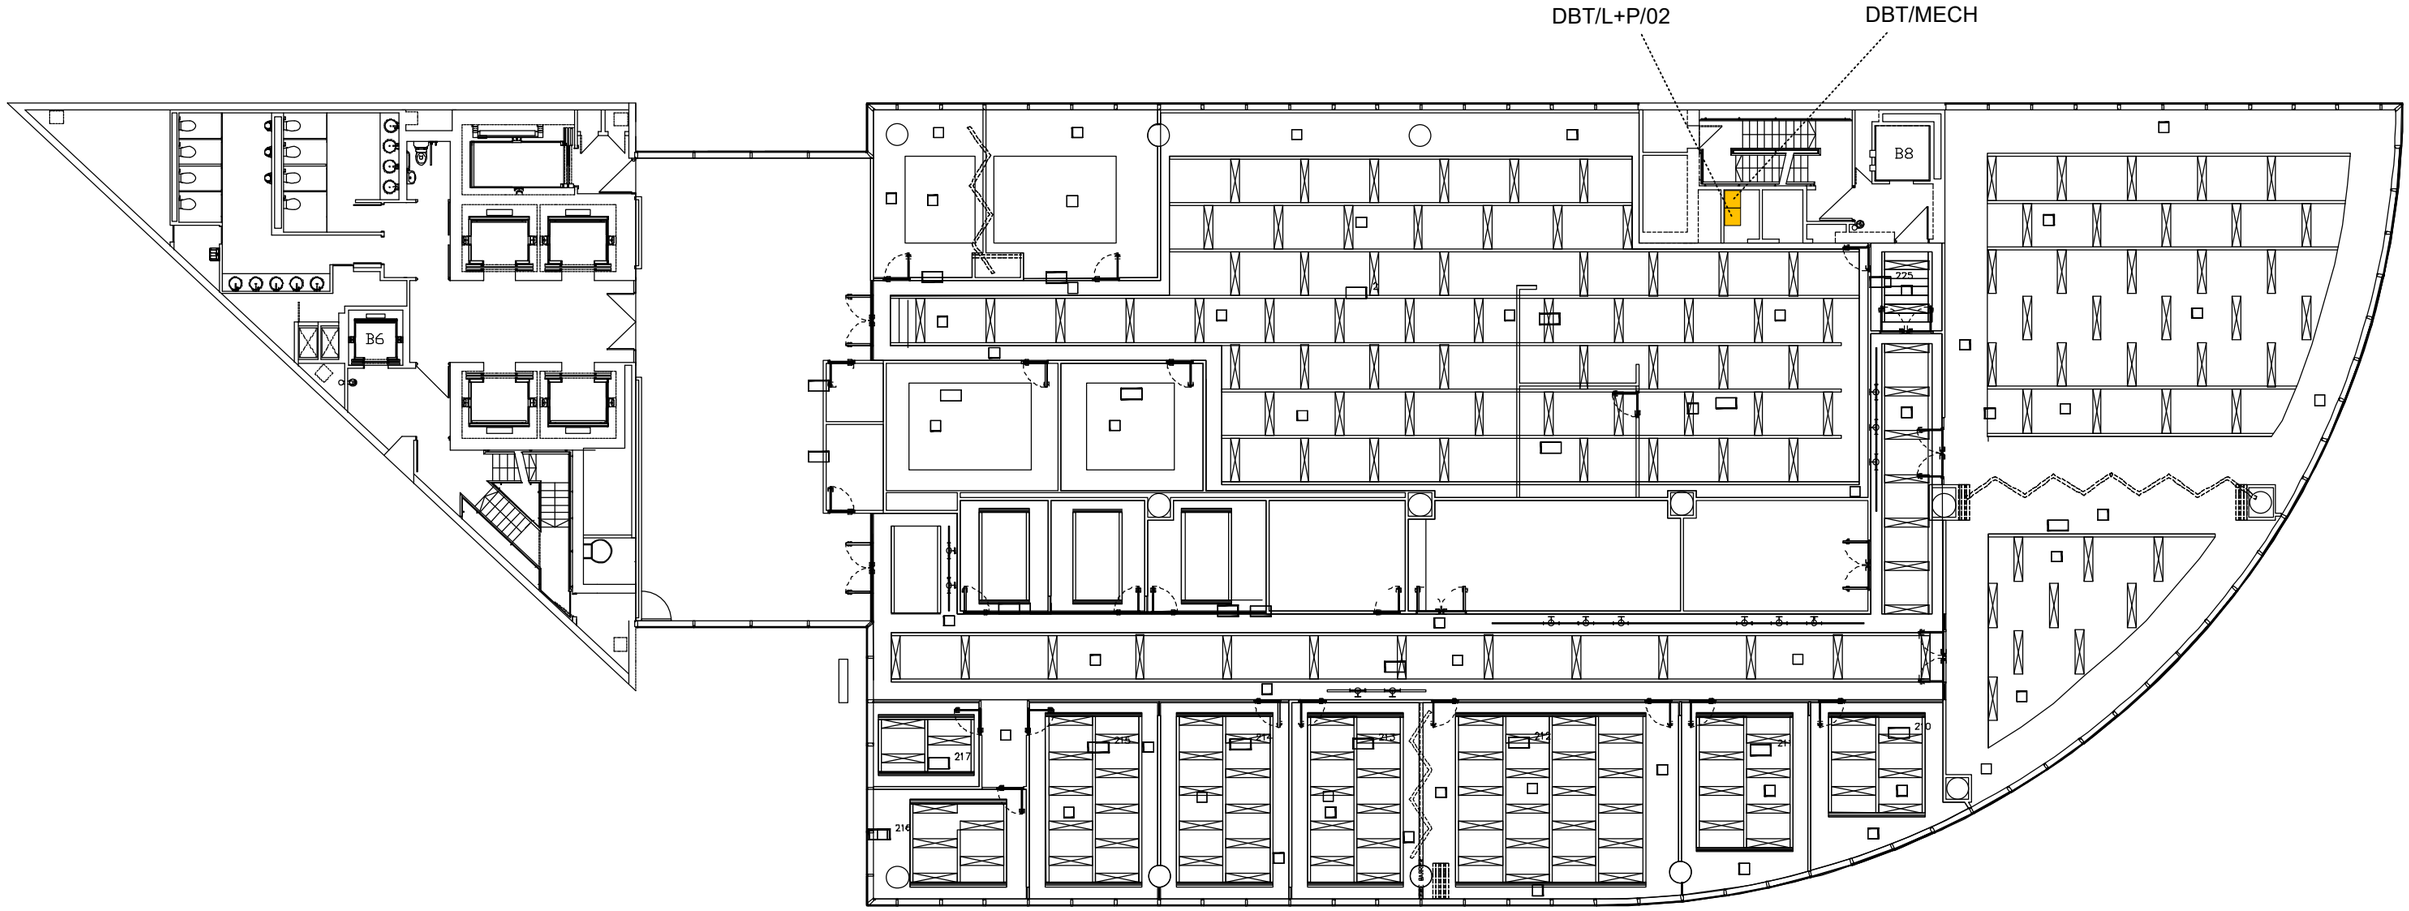

Legend


- CAT 5/6 Cables
- Modbus Network
- Electricity Meters
- Heat Meters
- Water Meters
- Gas Meters
- Modbus Gateway
- Distribution Board

knight CONTROLS ENERGY

Knight Controls Limited
8 Maltings Industrial Estate
Maltings Road
Battlesbridge
Essex
SS11 7RH
www.knightcontrols.co.uk

TITLE:: **Level 2**

SITE:	DRAWING No:	REVISION:
2 More London	161225	0
CLIENT:	DATE:	SHEET:
Smart Managed Solutions	December 2025	5 of 13

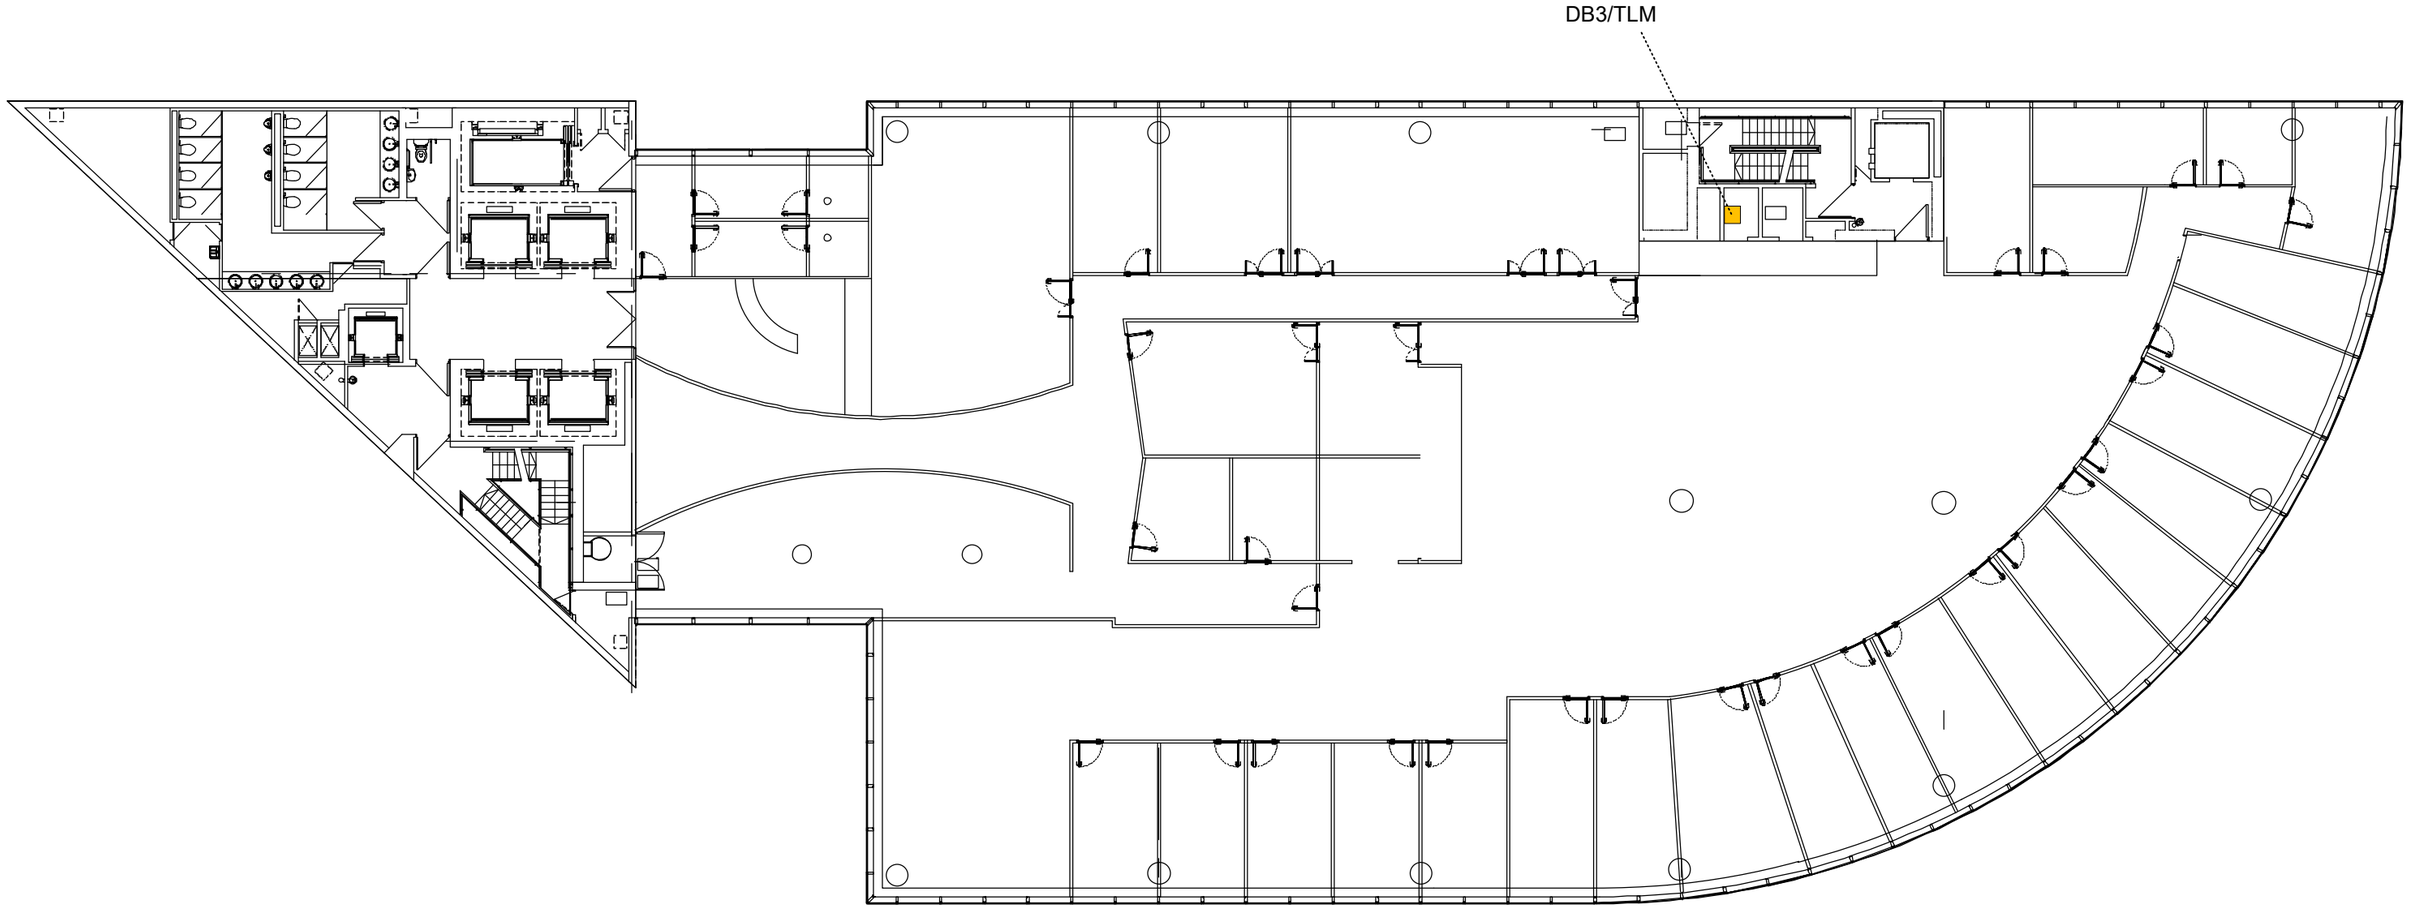

Legend


- CAT 5/6 Cables
- Modbus Network
- Electricity Meters
- Heat Meters
- Water Meters
- Gas Meters
- Modbus Gateway
- Distribution Board

Knight Controls Limited
8 Maltings Industrial Estate
Maltings Road
Battlesbridge
Essex
SS11 7RH
www.knightcontrols.co.uk

TITLE::

Level 3

SITE: **2 More London**	DRAWING No: 161225	REVISION: 0
CLIENT: **Smart Managed Solutions**	DATE: December 2025	SHEET: 6 of 13

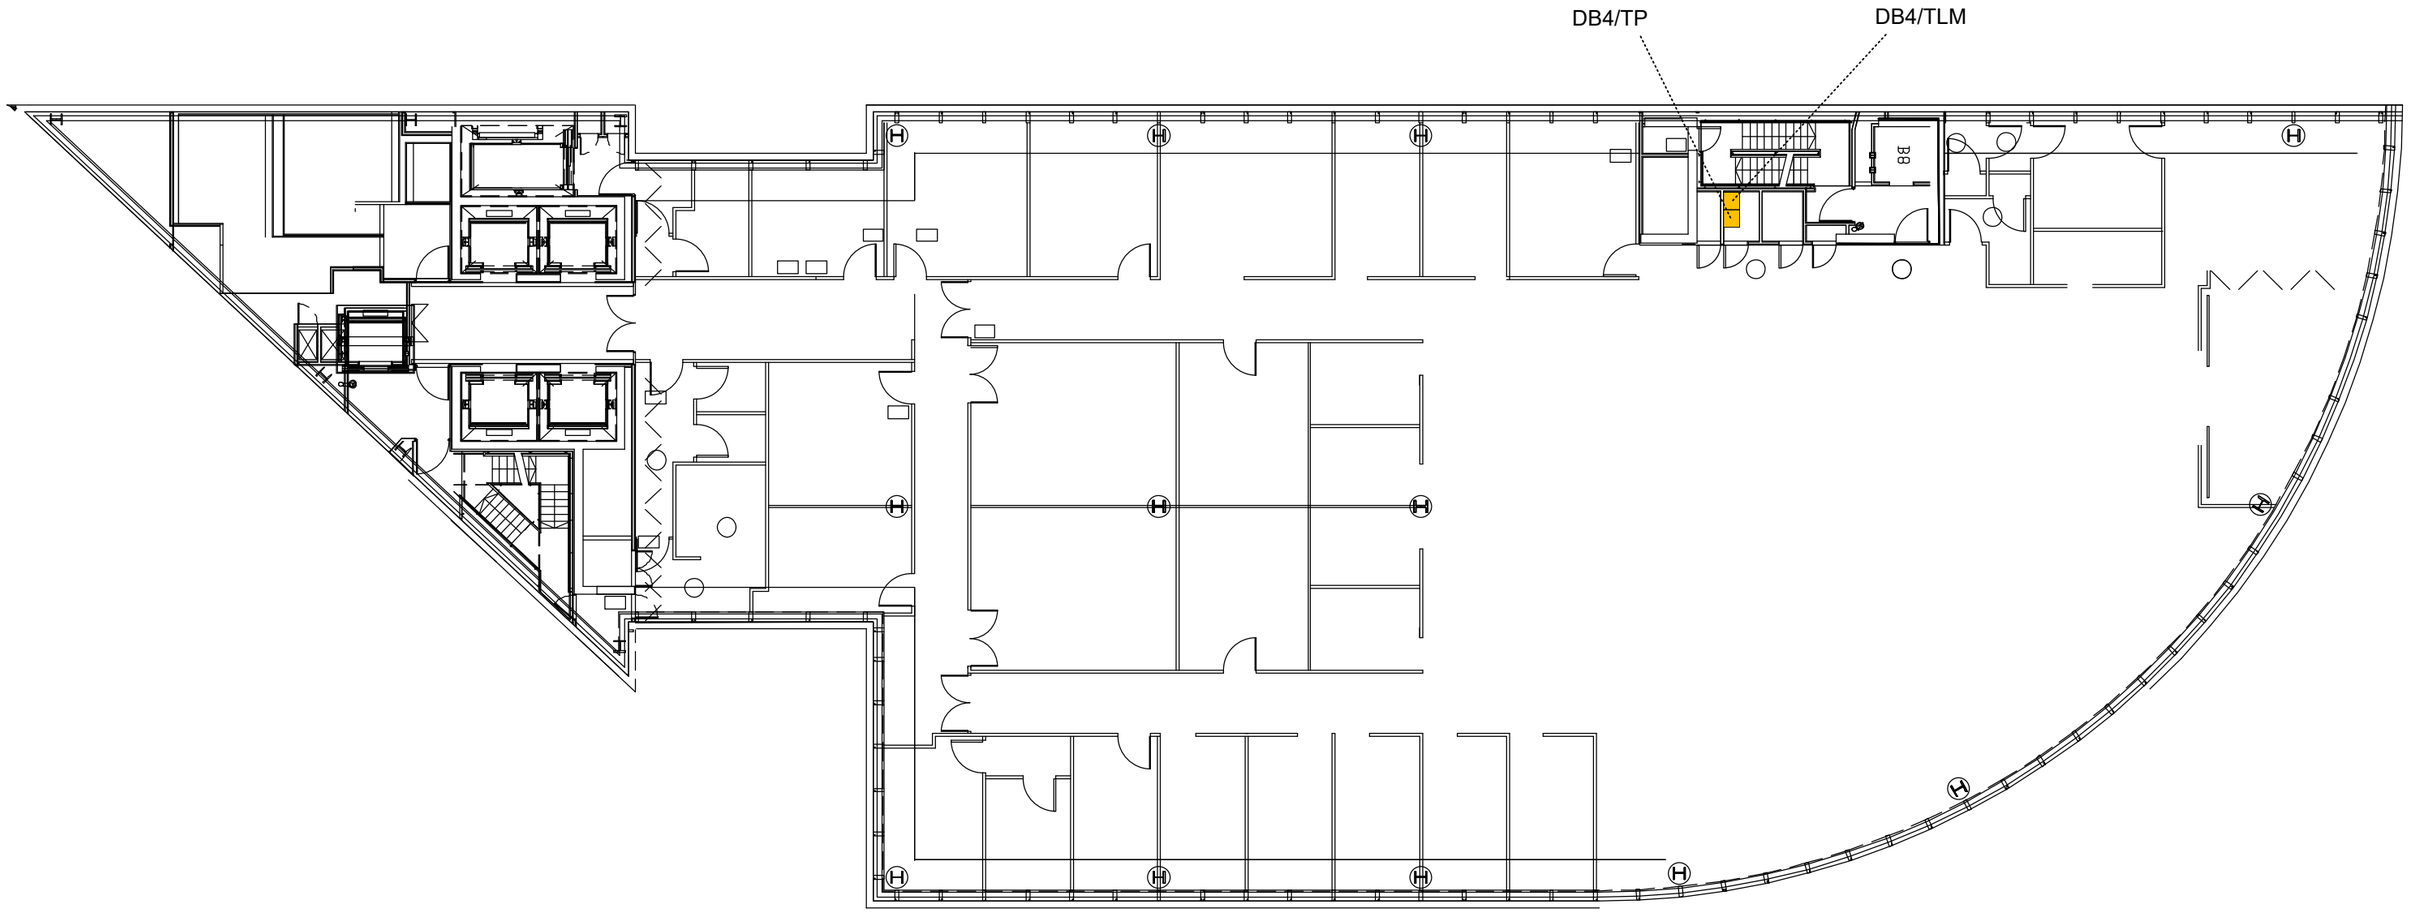

Legend

- CAT 5/6 Cables
- Modbus Network
- Electricity Meters
- Heat Meters
- Water Meters
- Gas Meters
- Modbus Gateway
- Distribution Board


knight CONTROLS ENERGY

Knight Controls Limited
8 Maltings Industrial Estate
Maltings Road
Battlesbridge
Essex
SS11 7RH
www.knightcontrols.co.uk

TITLE::

Level 4

SITE:	DRAWING No:	REVISION:
2 More London	161225	0
CLIENT:	DATE:	SHEET:
Smart Managed Solutions	December 2025	7 of 13

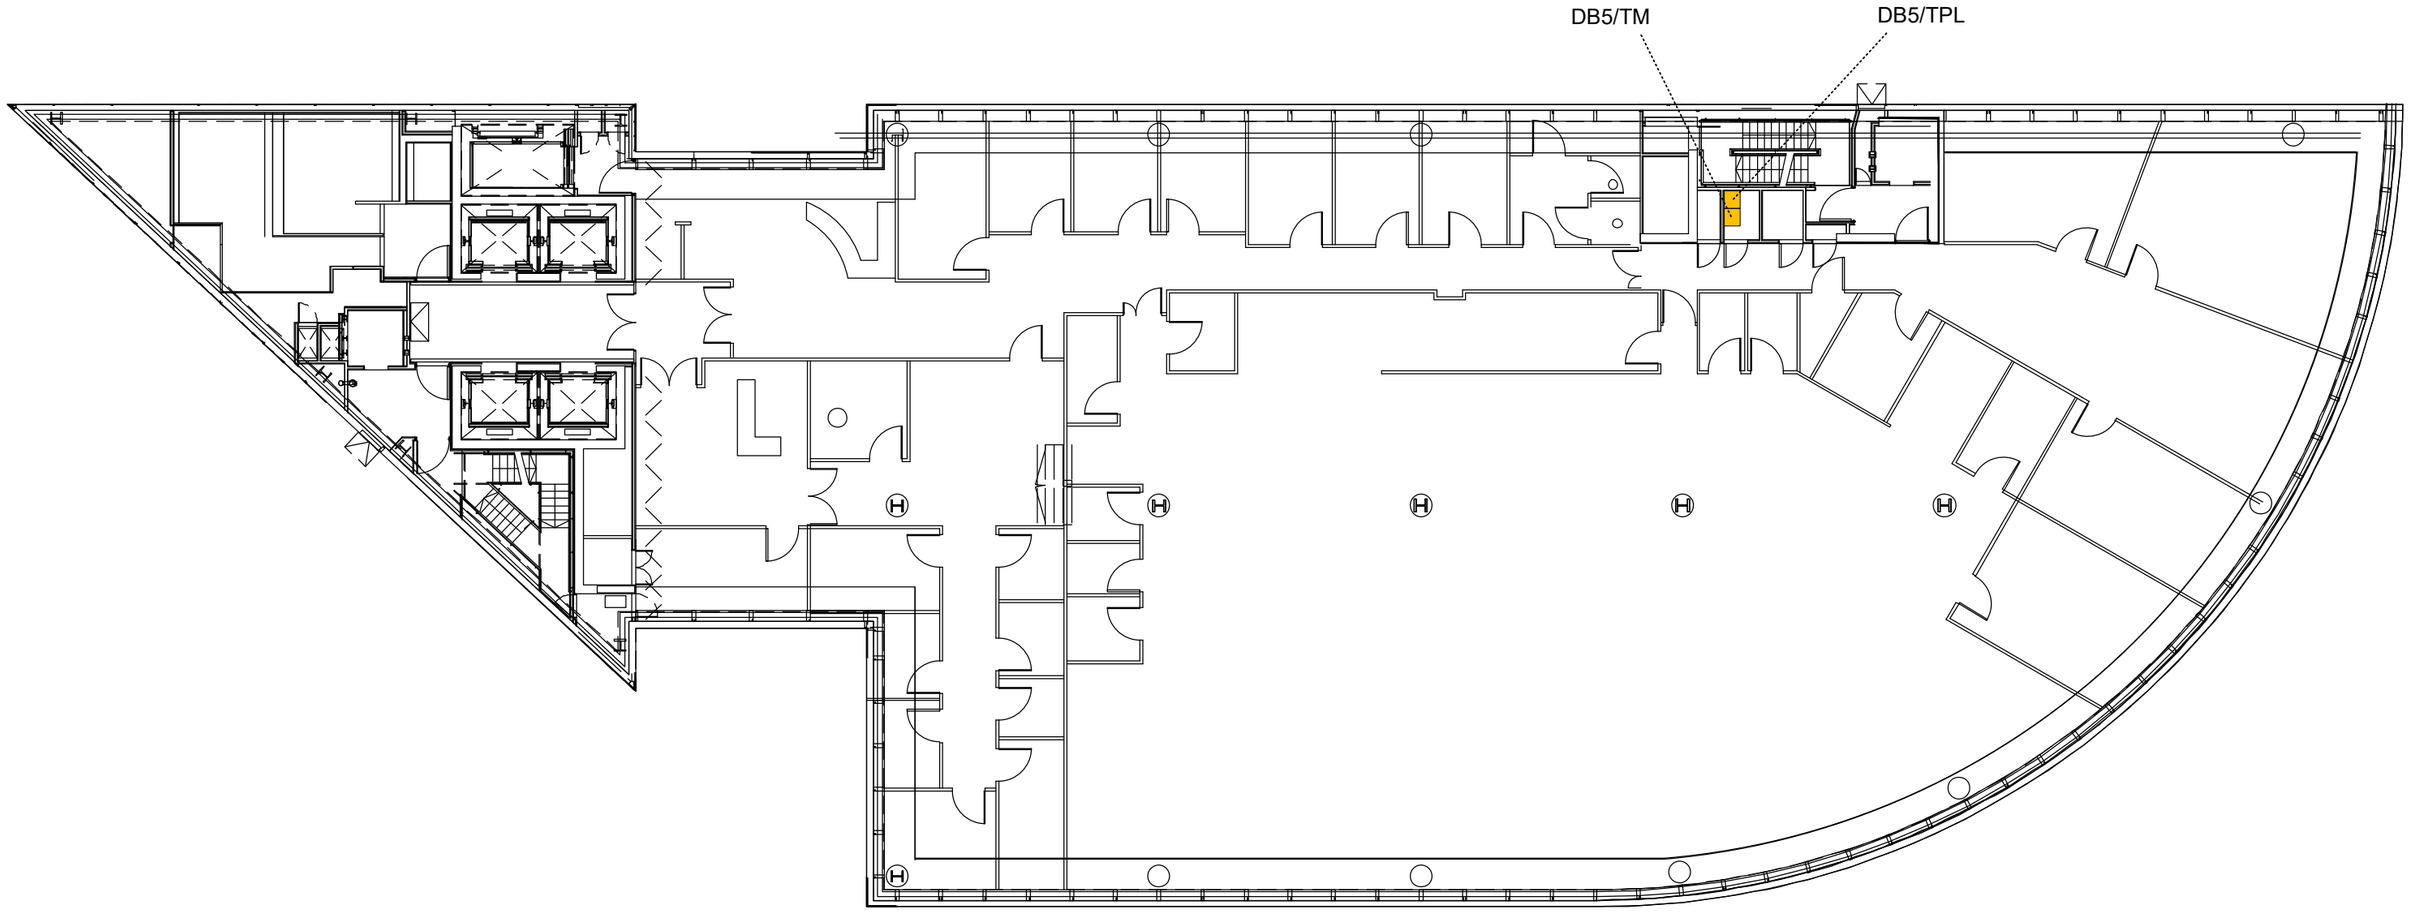

Legend


- CAT 5/6 Cables
- Modbus Network
- Electricity Meters
- Heat Meters
- Water Meters
- Gas Meters
- Modbus Gateway
- Distribution Board

knight CONTROLS ENERGY

Knight Controls Limited
8 Maltings Industrial Estate
Maltings Road
Battlesbridge
Essex
SS11 7RH
www.knightcontrols.co.uk

TITLE:: **Level 5**

SITE: **2 More London**	DRAWING No: 161225	REVISION: 0
CLIENT: **Smart Managed Solutions**	DATE: December 2025	SHEET: 8 of 13

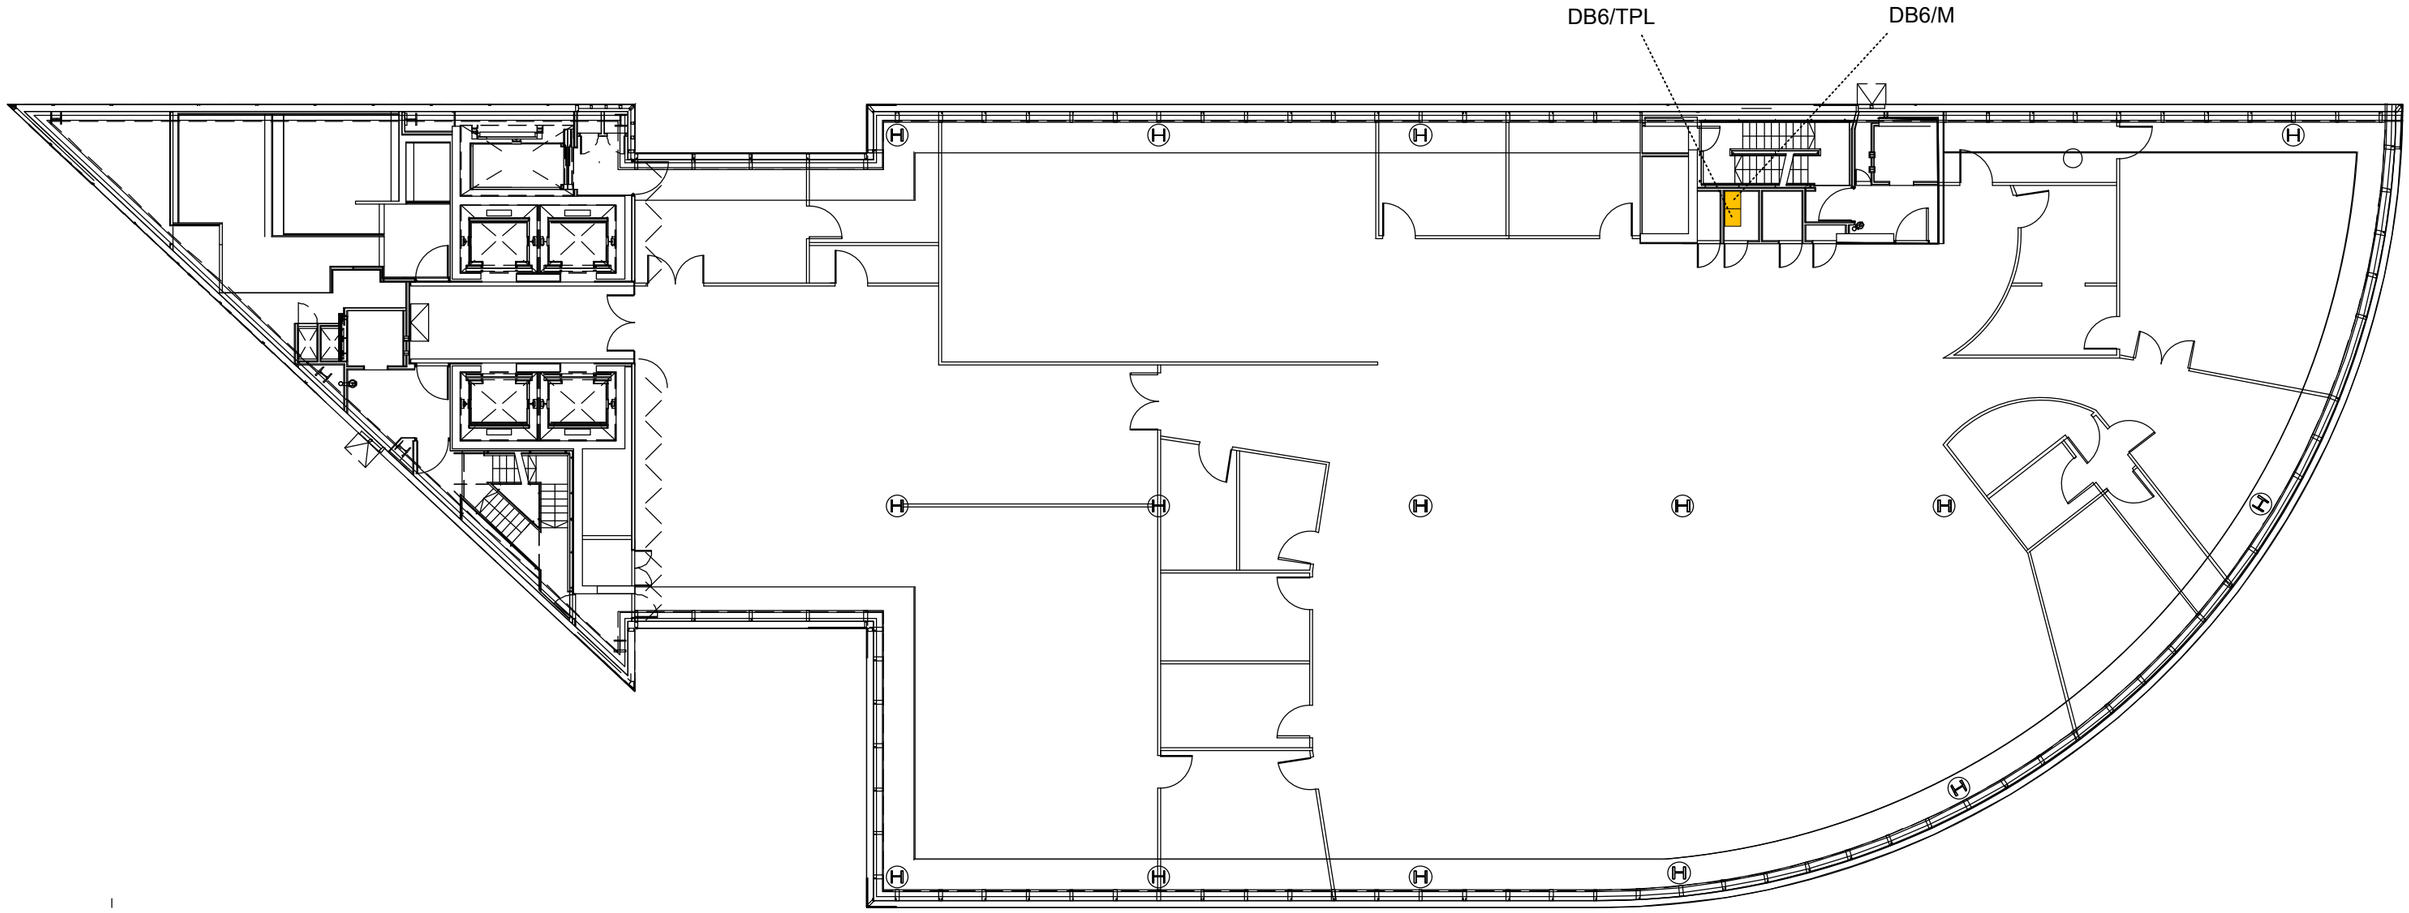

Legend

- CAT 5/6 Cables
- Modbus Network
- Electricity Meters
- Heat Meters
- Water Meters
- Gas Meters
- Modbus Gateway
- Distribution Board


knight CONTROLS ENERGY

Knight Controls Limited
8 Maltings Industrial Estate
Maltings Road
Battlesbridge
Essex
SS11 7RH
www.knightcontrols.co.uk

TITLE::

Level 6

SITE:	DRAWING No:	REVISION:
2 More London	161225	0
CLIENT:	DATE:	SHEET:
Smart Managed Solutions	December 2025	9 of 13

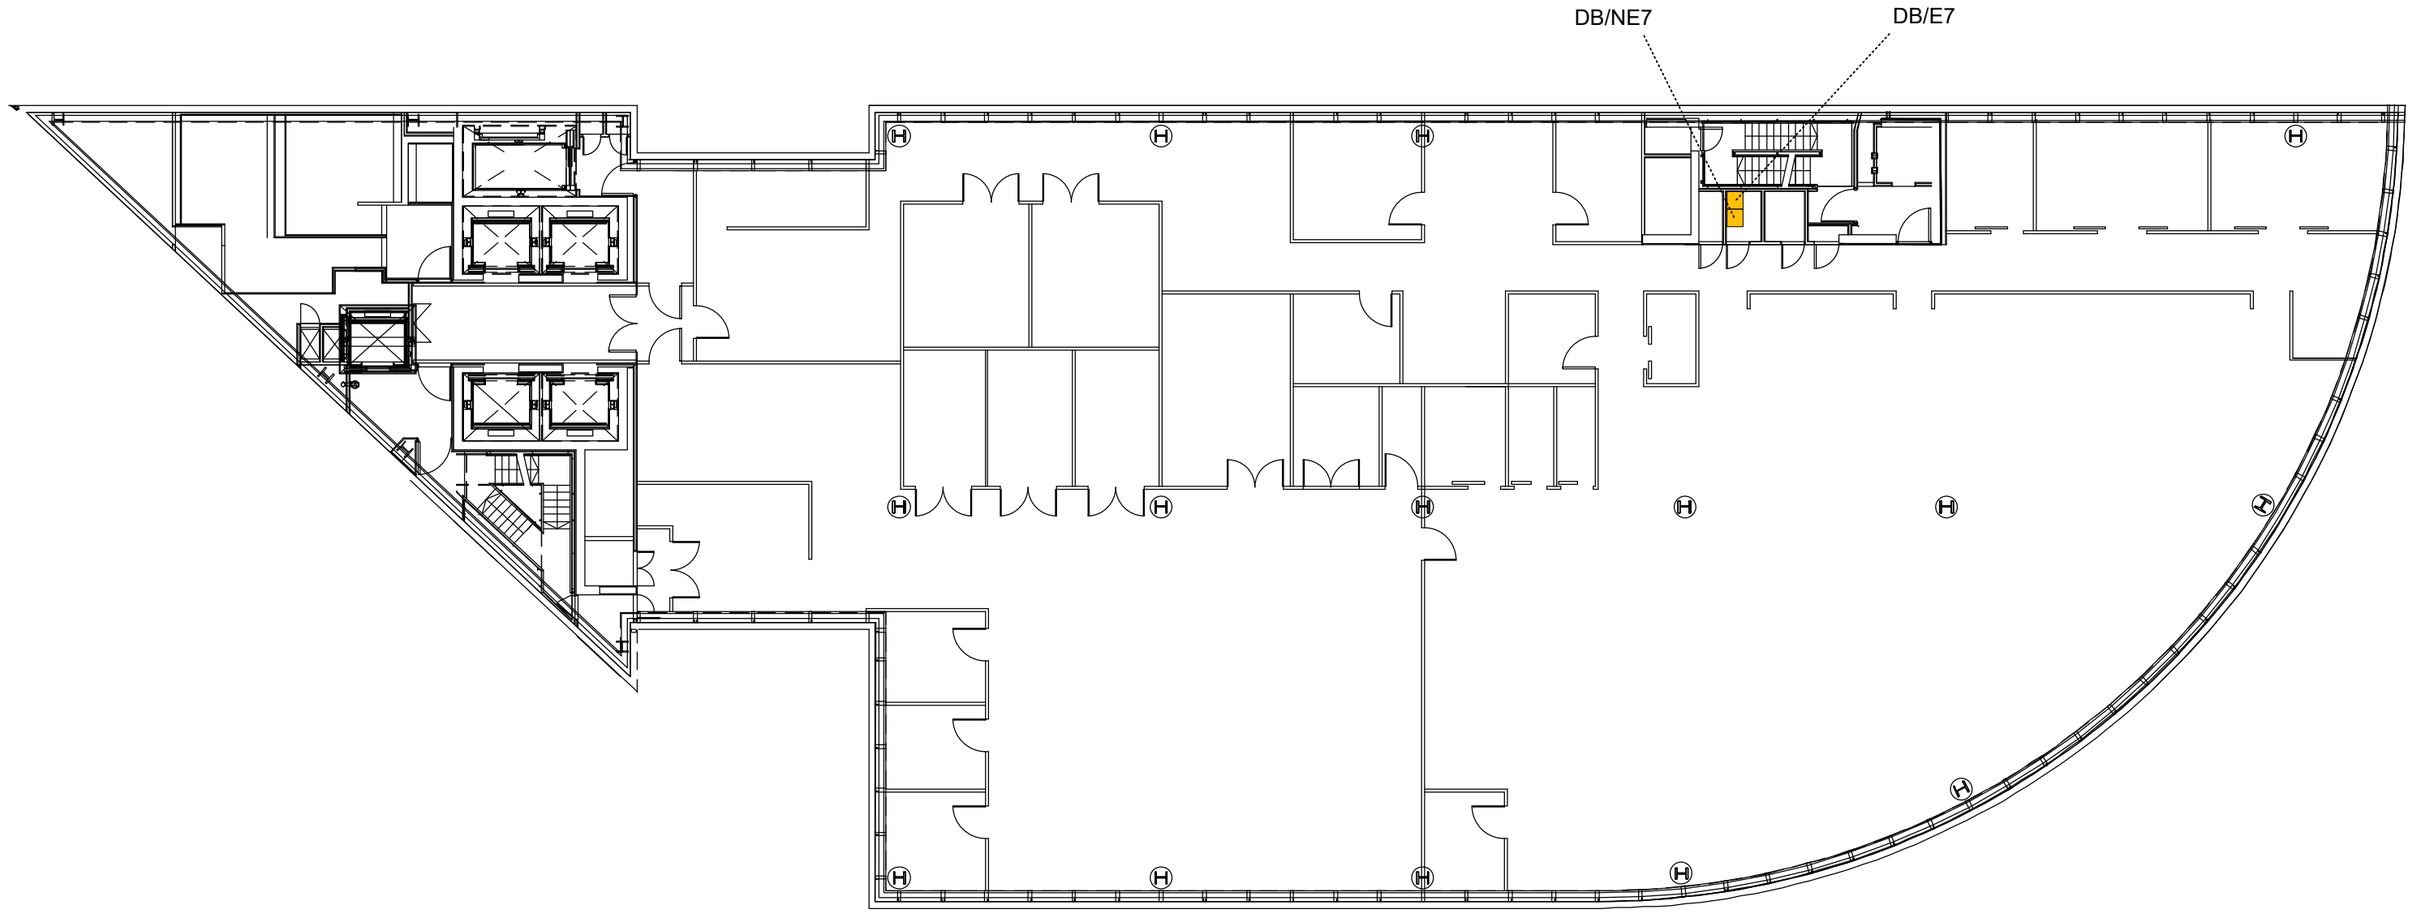

Legend


- CAT 5/6 Cables
- Modbus Network
- Electricity Meters
- Heat Meters
- Water Meters
- Gas Meters
- Modbus Gateway
- Distribution Board

Knight Controls Limited
8 Maltings Industrial Estate
Maltings Road
Battlesbridge
Essex
SS11 7RH
www.knightcontrols.co.uk

TITLE::

Level 7

SITE: **2 More London**	DRAWING No: 161225	REVISION: 0
CLIENT: **Smart Managed Solutions**	DATE: December 2025	SHEET: 10 of 13

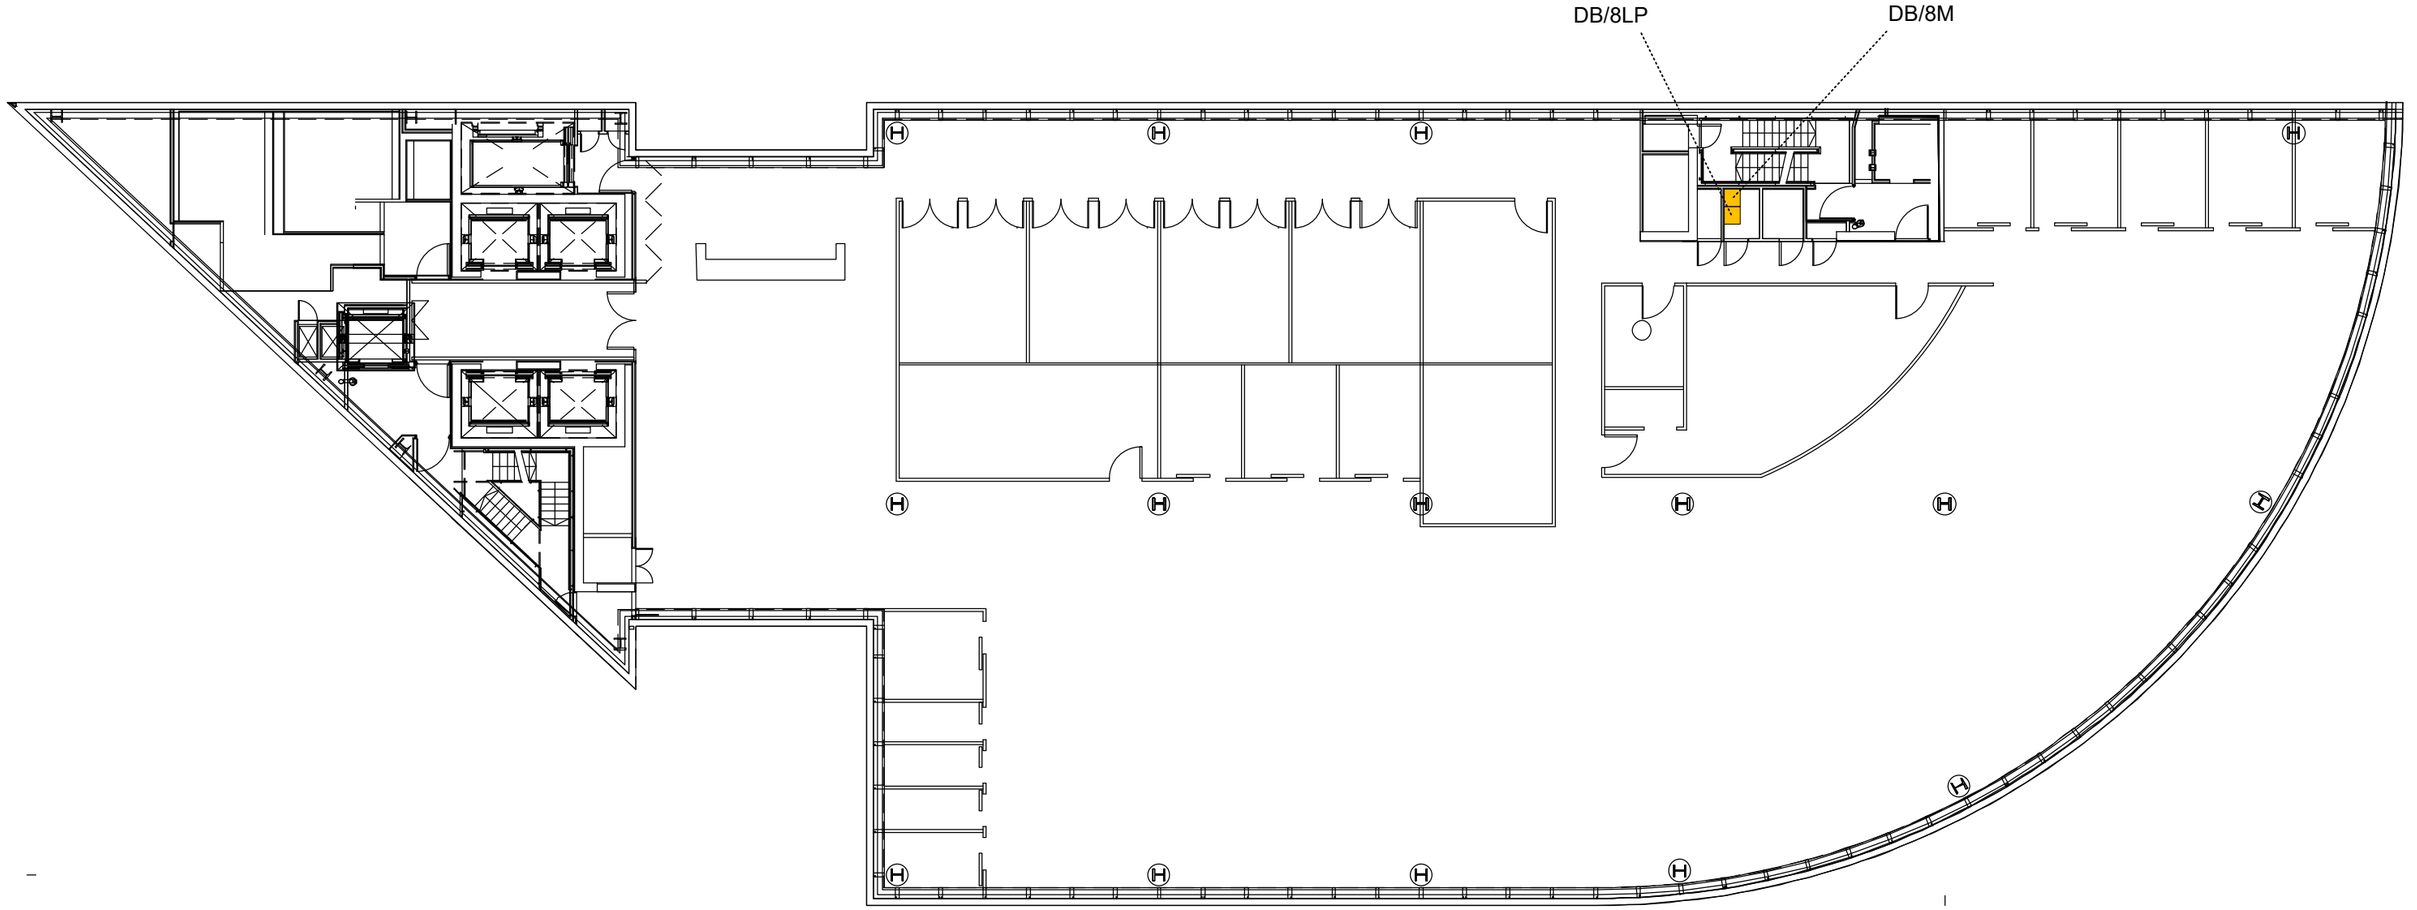

Legend


- CAT 5/6 Cables
- Modbus Network
- Electricity Meters
- Heat Meters
- Water Meters
- Gas Meters
- Modbus Gateway
- Distribution Board

Knight Controls Limited
8 Maltings Industrial Estate
Maltings Road
Battlesbridge
Essex
SS11 7RH
www.knightcontrols.co.uk

TITLE::

Level 8

SITE: **2 More London**	DRAWING No: 161225	REVISION: 0
CLIENT: **Smart Managed Solutions**	DATE: December 2025	SHEET: 11 of 13

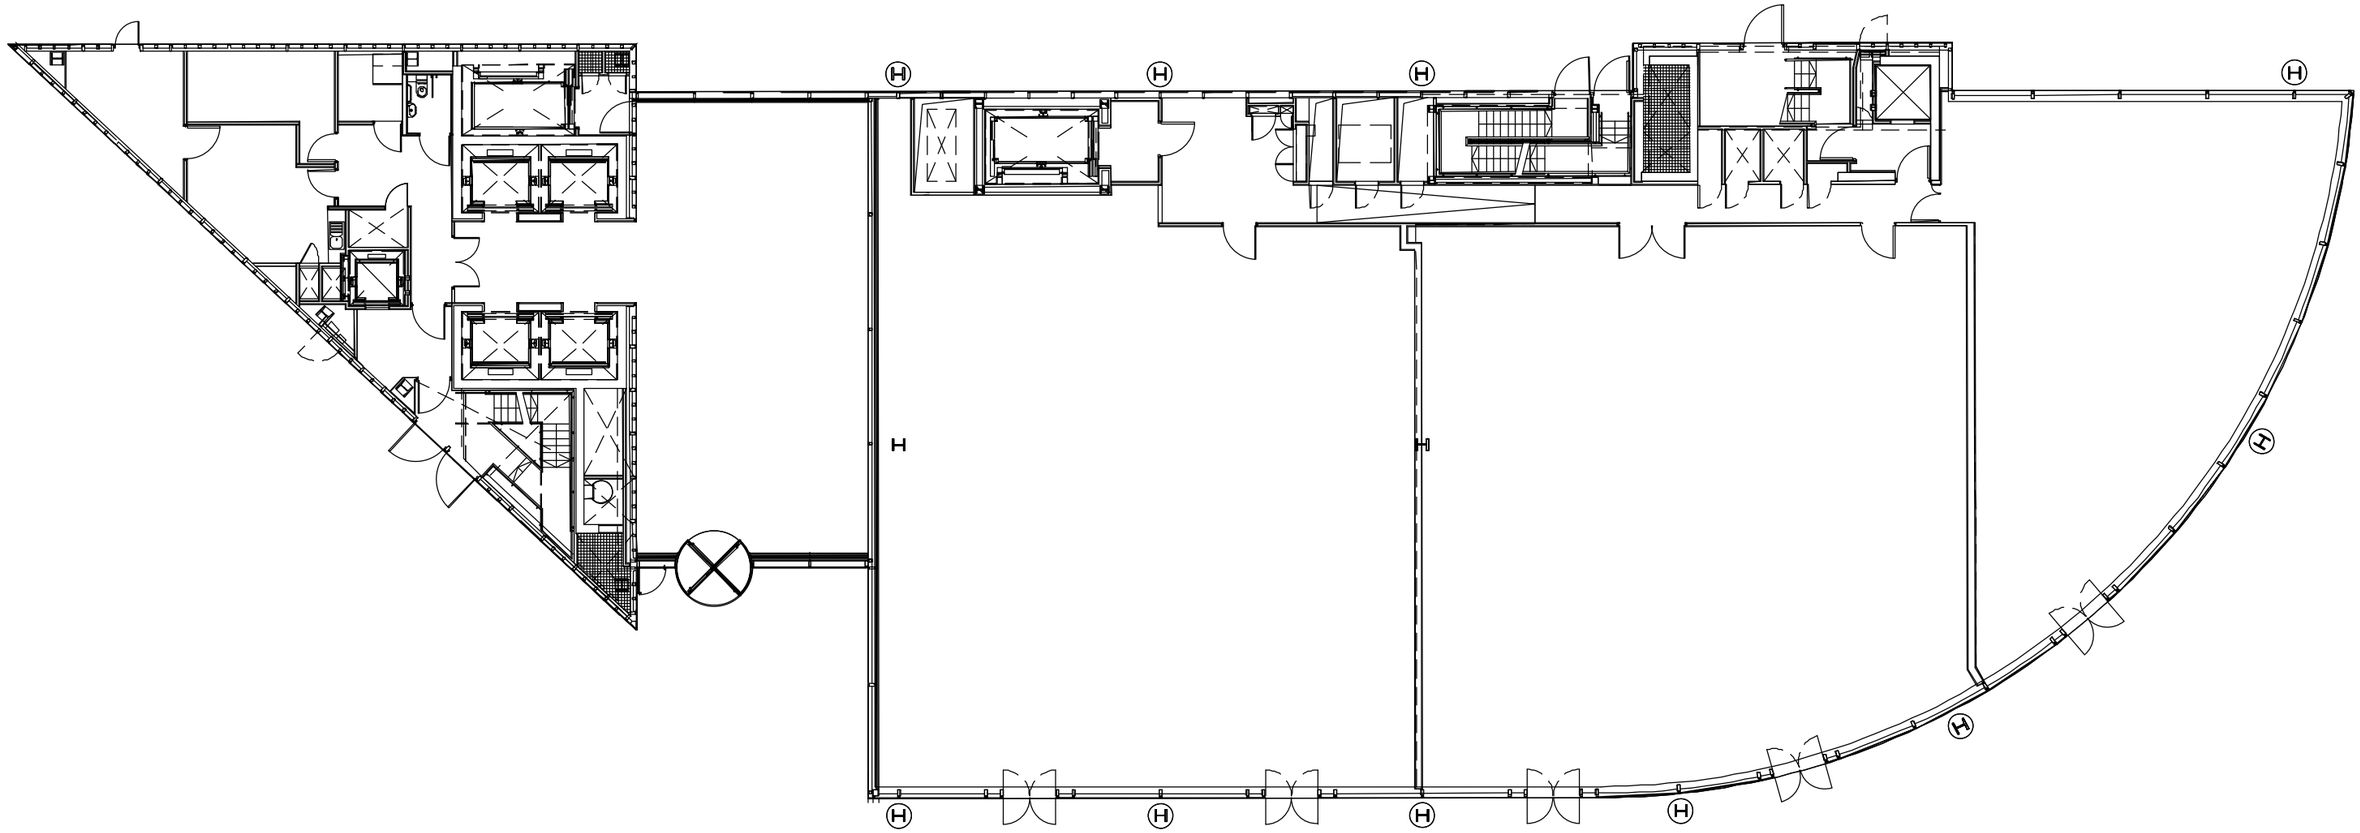

Legend


CAT 5/6 Cables	
Modbus Network	
Electricity Meters	
Heat Meters	
Water Meters	
Gas Meters	
Modbus Gateway	
Distribution Board	

Knight Controls Limited
8 Maltings Industrial Estate
Maltings Road
Battlesbridge
Essex
SS11 7RH
www.knightcontrols.co.uk

TITLE::

Level 9

SITE: **2 More London**	DRAWING No: 161225	REVISION: 0
CLIENT: **Smart Managed Solutions**	DATE: December 2025	SHEET: 12 of 13

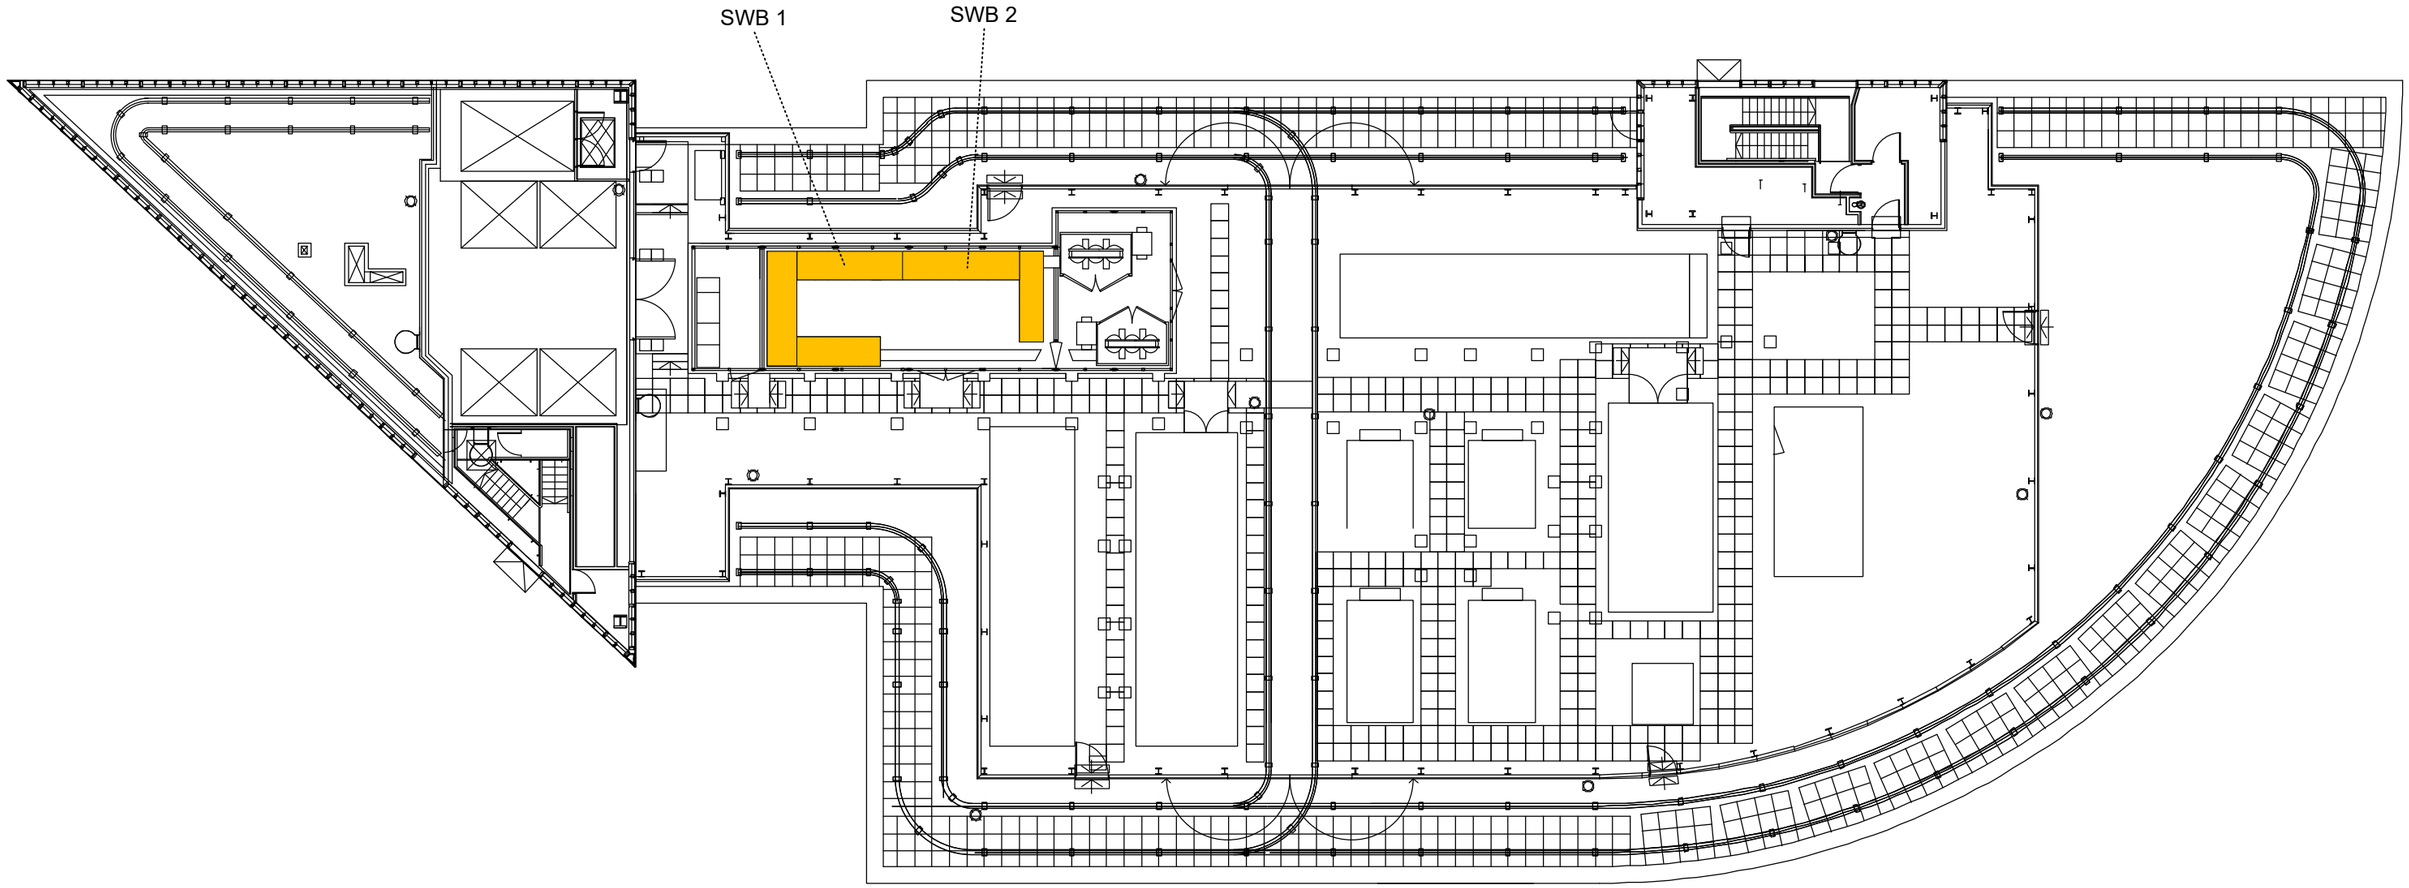

Legend

- CAT 5/6 Cables
- Modbus Network
- Electricity Meters
- Heat Meters
- Water Meters
- Gas Meters
- Modbus Gateway
- Distribution Board

knight CONTROLS ENERGY

Knight Controls Limited
8 Maltings Industrial Estate
Maltings Road
Battlesbridge
Essex
SS11 7RH
www.knightcontrols.co.uk

TITLE::

Roof

SITE:	DRAWING No:	REVISION:
2 More London	161225	0
CLIENT:	DATE:	SHEET:
Smart Managed Solutions	December 2025	13 of 13